






0 CDO GROUND FLOOR PLAN Copy 3
1 : 175

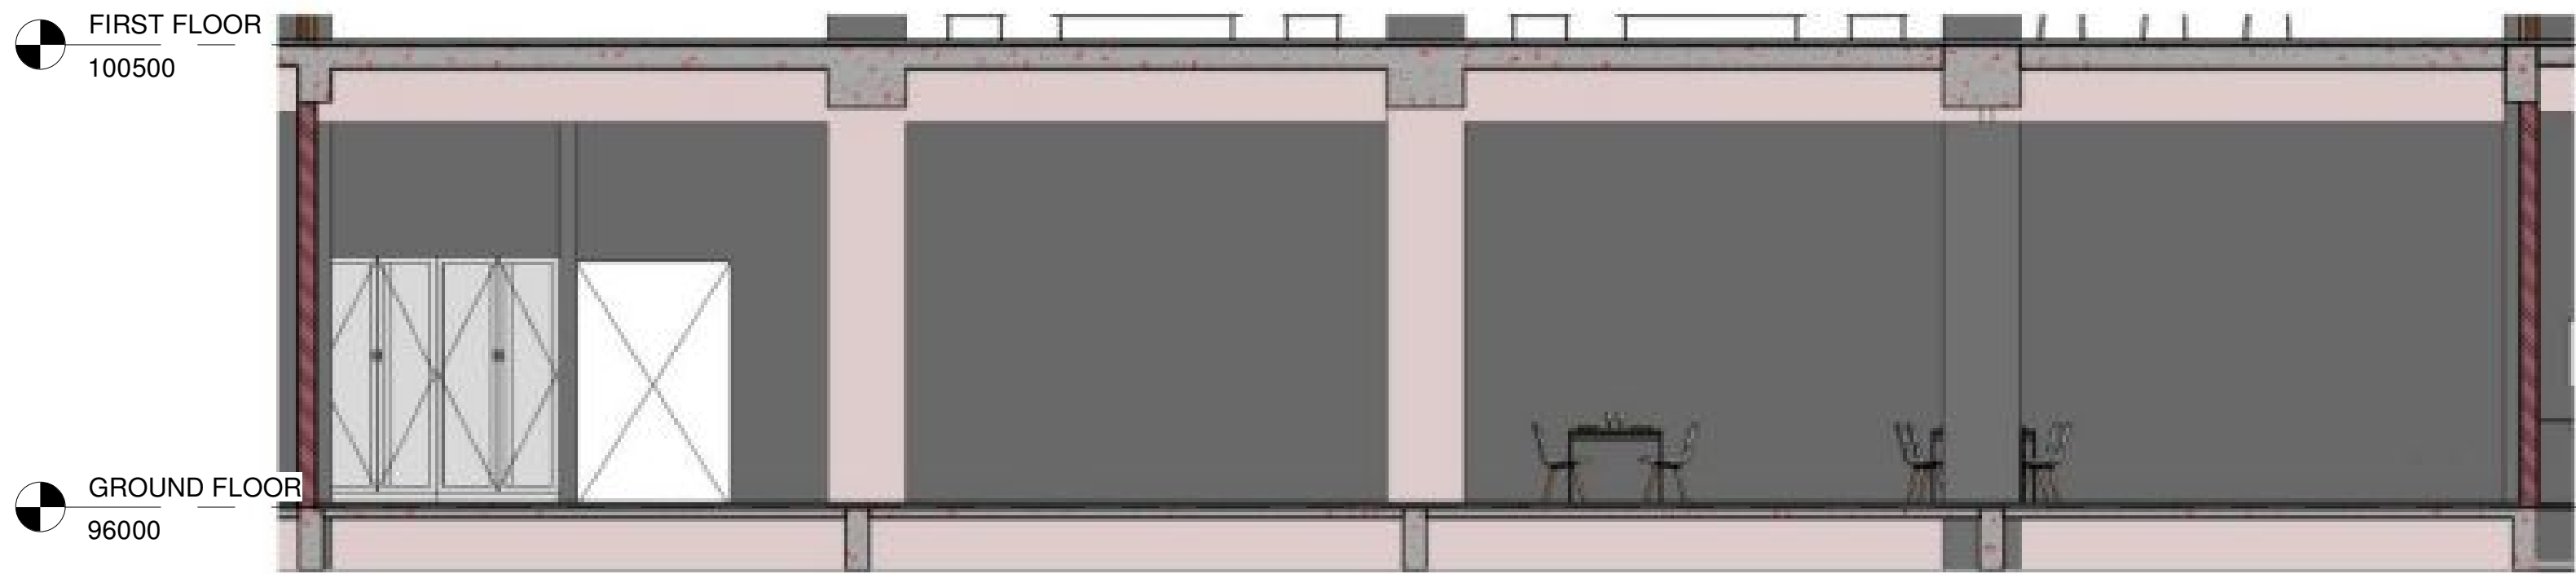


34 Elevation - 34
1 : 60

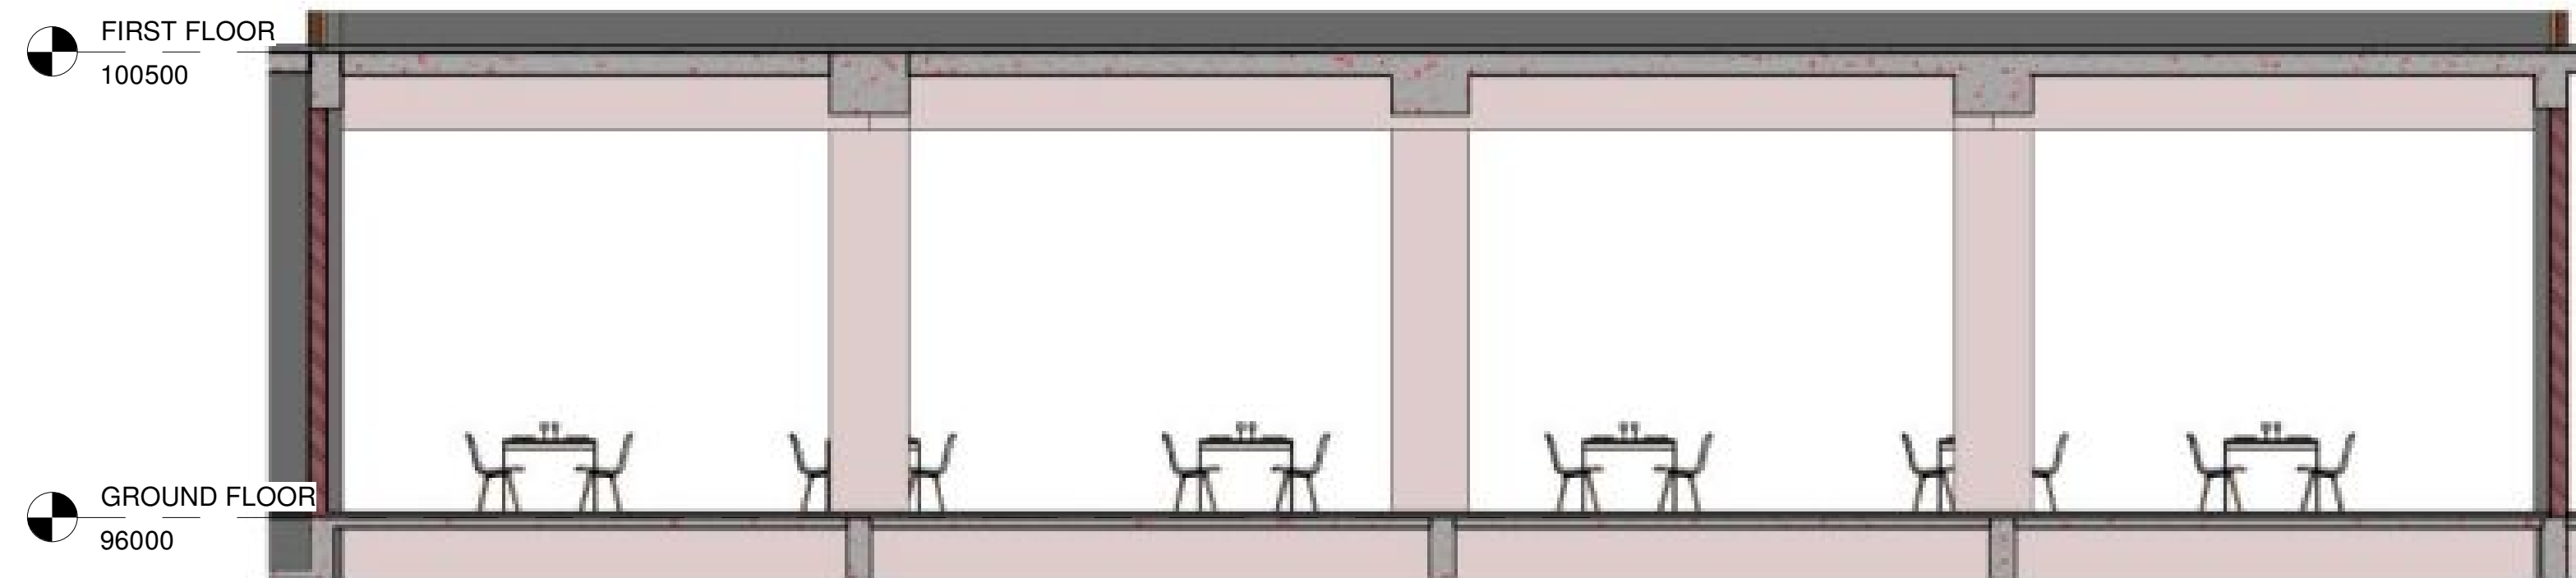

36 Elevation - 36
1 : 60

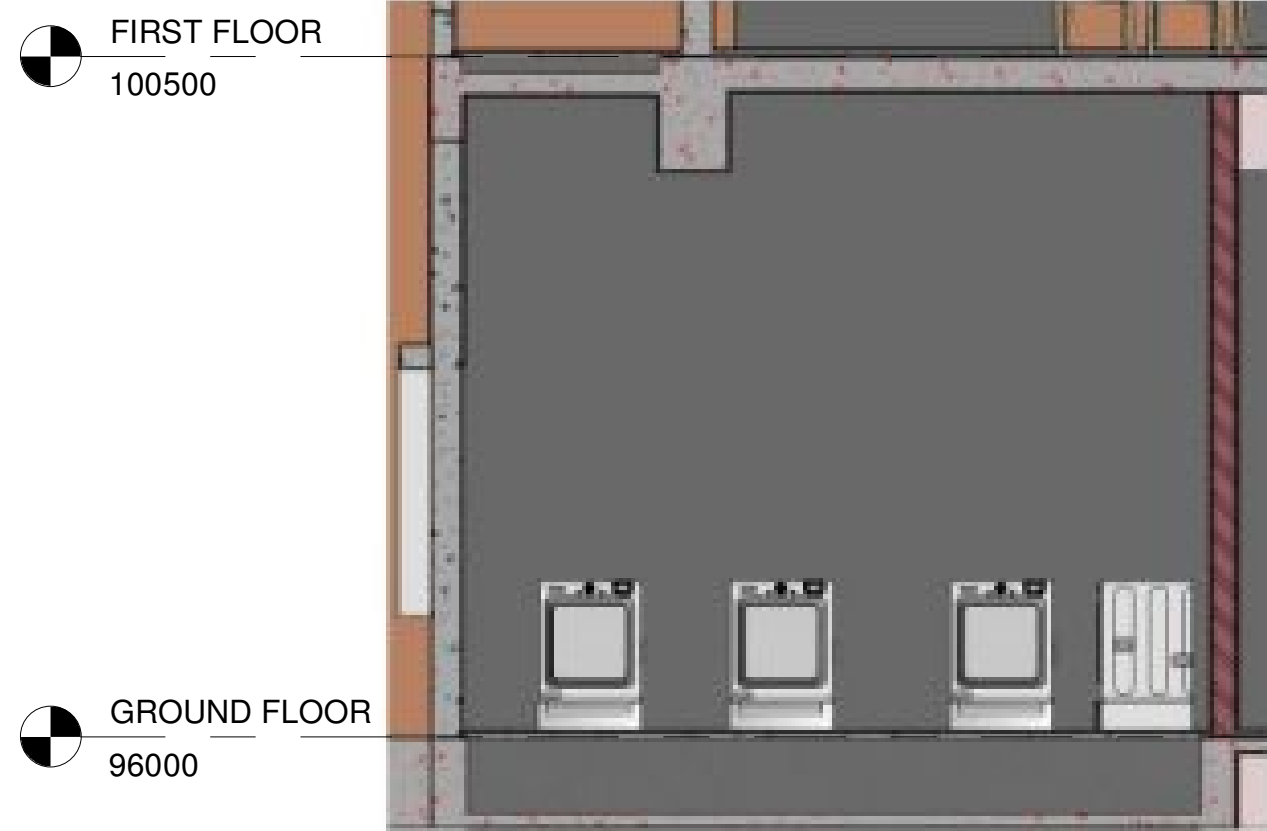


29 Elevation - 29
1 : 50

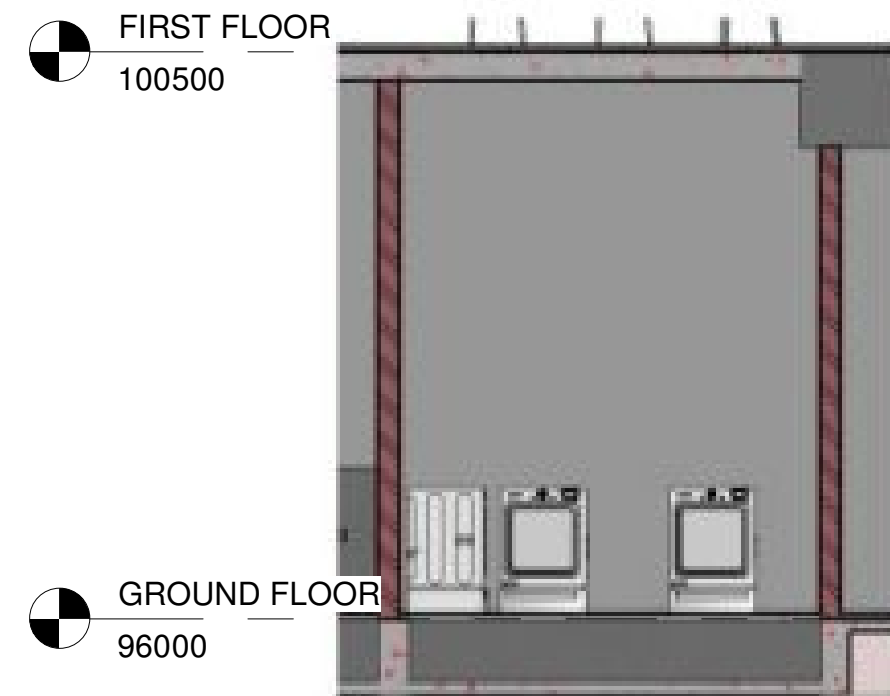


32 Elevation - 32
1 : 60



30 Elevation - 30
1 : 50

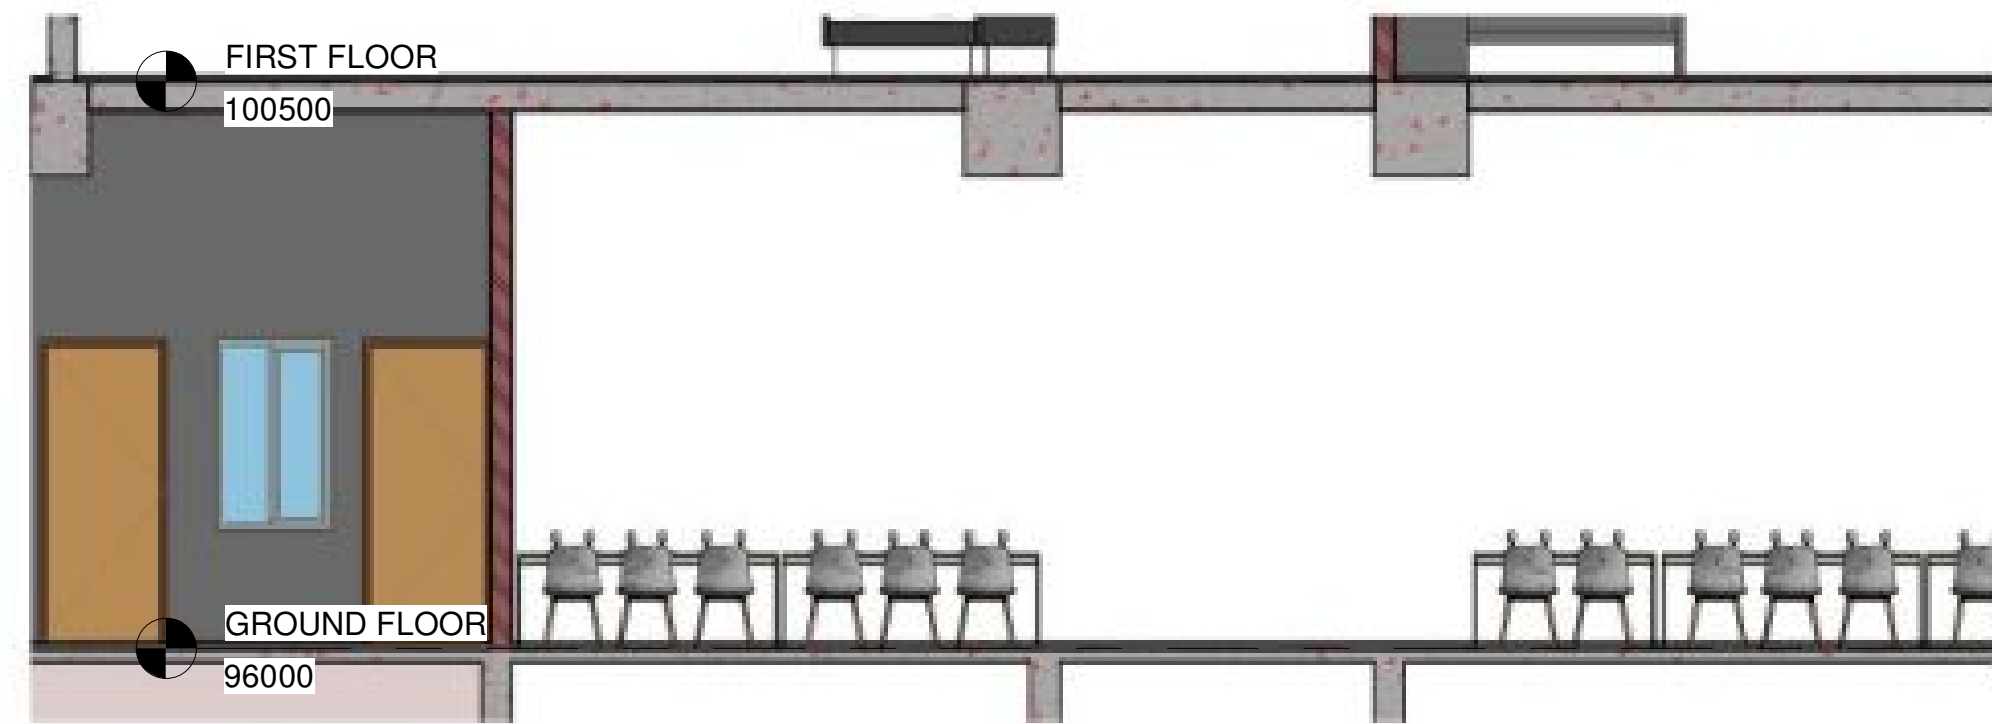

33 Elevation - 33
1 : 60

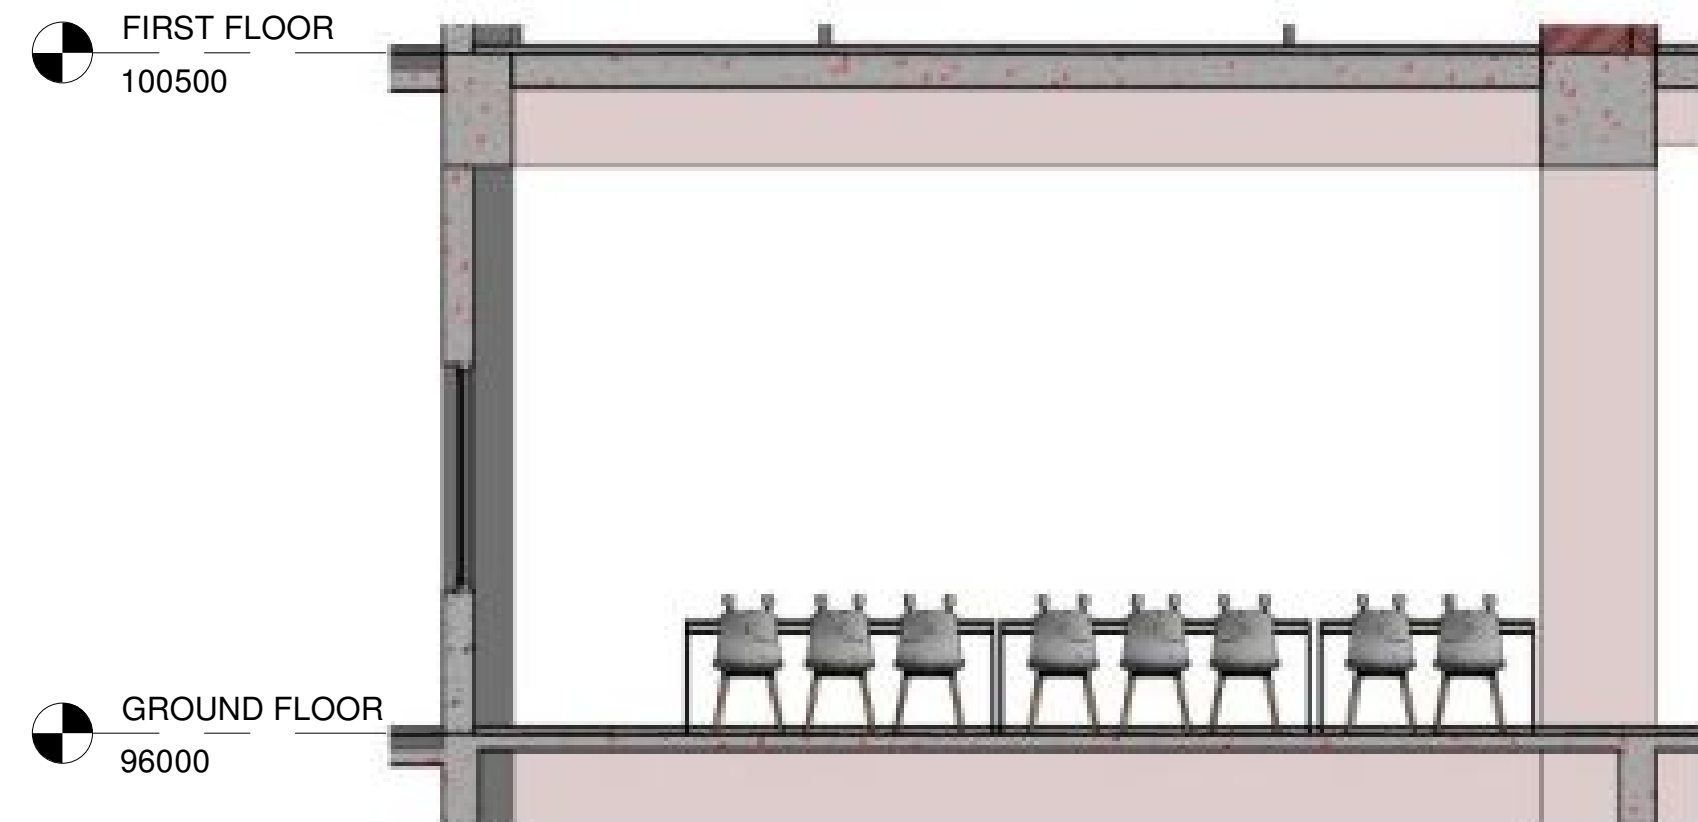

35 Elevation - 35
1 : 50



31 Elevation - 31
1 : 60

PROJECT : NSG CAMPUS																
GENERAL NOTES : 1. ALL DIMENSIONS ARE IN MILLIMETER UNLESS STATED OTHERWISE. 2. NO DIMENSION IS TO BE SCALED OFF THE DRAWING. 3. THIS DRAWING TO BE READ IN CONJUNCTION WITH ALL RELEVANT THIS DRAWING TO BE READ IN CONJUNCTION WITH ALL RELEVANT DETAILS. 4. ANY DISCREPANCY IN DRAWING, TO BE BROUGHT TO THE NOTICE OF ARCHITECTS BEFORE COMMENCEMENT OF WORK. 5. FOR ALL STAIRS, ELEVATORS, TOILETS - REF SEPARATE DETAILS. 6. FOR ALL SERVICE DRAWINGS - REFER SEPARATE DETAILS.																
KEY PLAN:																
																
SIGNED/STAMPED BY : BPR INFRASTRUCTURE PRIVATE LIMITED																
																
SIGNED/STAMPED BY : B DESIGN STUDIOS																
ISSUE/REVISION																
<table><tr><th>IR</th><th>DATE</th><th>DESCRIPTION</th></tr><tr><td> </td><td> </td><td> </td></tr><tr><td> </td><td> </td><td> </td></tr><tr><td> </td><td> </td><td> </td></tr><tr><td> </td><td> </td><td> </td></tr></table>		IR	DATE	DESCRIPTION												
IR	DATE	DESCRIPTION														
CLIENT CPWD CENTRAL PUBLIC WORKS DEPARTMENT																
EPC CONTRACTOR  M/S BPR INFRASTRUCTURE PRIVATE LIMITED Plot No. 103 & 104, 1st Floor Capital Park, Road, Madhapur, Hyderabad, Telangana - 500081																
EPC ARCHITECT  B DESIGN STUDIOS 3rd Floor, ANR Gurni Square Plot No. 103, Road, Jalandhar, Ludhiana, Punjab - 141001 Website: www.bdesignstudios.in Phone: 98100-88001																
EPC STRUCTURAL & MEP CONSULTANT  SUVM ENGINEERING SERVICES P-2/4 N Square, Madhapur, Hyderabad, Telangana - 500081 Phone: 92201-8040																
PROJECT : Construction of NSG Regional Hub at Lekhawadi, Gandhinagar, Gujarat (SH) - Construction of 104 nos Type-II, 40 nos Type-III, 14 nos Type-IV, 2 nos Type-V, 1 no. Administrative building cum Lecture hall, 1 no. Officers mess, 1 no. AC mess, 1 no. 280 men CDO barracks, 1 no. Quarter Guard, 1 no. MI Room cum Canteen cum Pre Primary School, 1 no. Electric substation, 1 no. STP, UG sump and 2 nos. Pump room including Internal Water Supply, Sanitary installation and Electrical work.External Service connection of Civil & Electrical, Internal roads, Cement Concrete pavement, Foot path, Storm water drains, Culverts, Retaining wall, etc. and all civil services and E & M services in Engineering, Procurement and Construction mode-I, Package-II). Agreement No: 01/CE/EE/(O)GNR-II/2025-26																
BLOCK : CDO BARRACKS																
DRAWING TITLE : CDO BARRACKS LIVING AREA SECTIONS																
DESIGN : SATHYA APPROVED : RAJESH																
SCALE : 1:75 DRAWN : MEGHANA																
DATE : 16-04-2026 CHECKED : SATHYA																
DRAWING NO : A103																
PROJECT NO	SHEET SIZE															
006	A1															
CONSTRUCTION	REVISION															
C	R0															