





1 TERRACE FLOOR
1 : 100

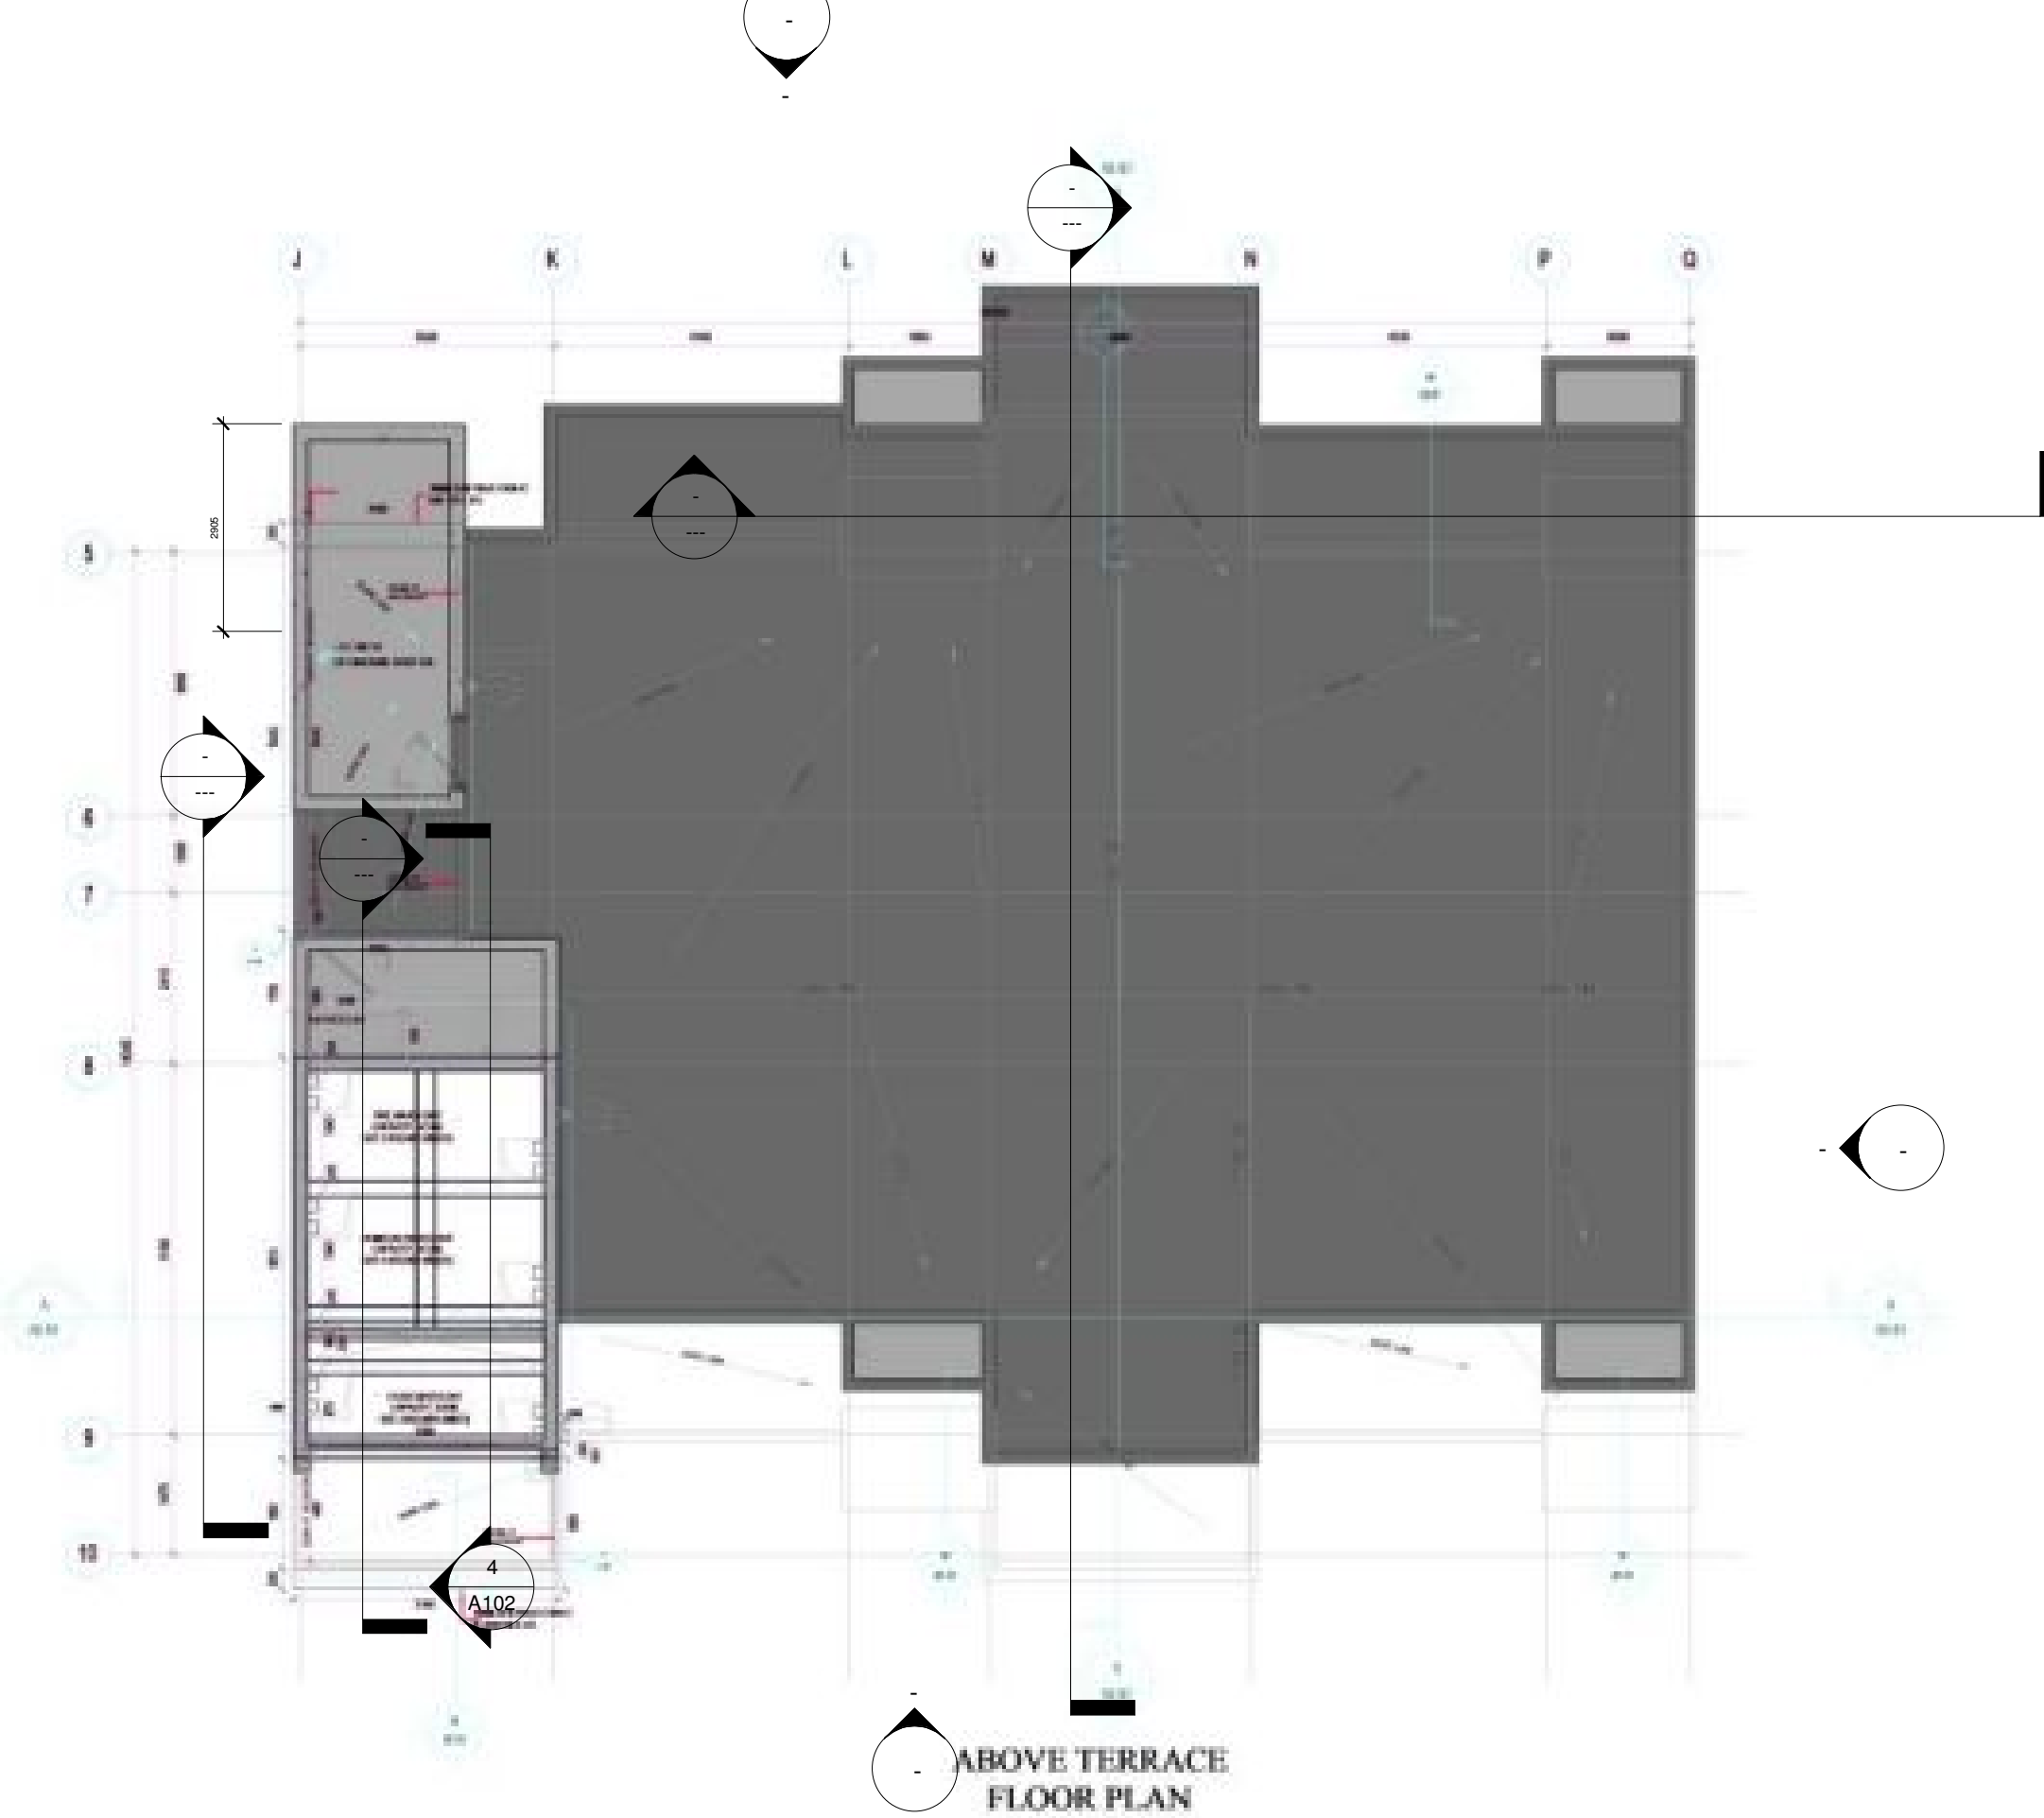

2 LMR SSL
1 : 100

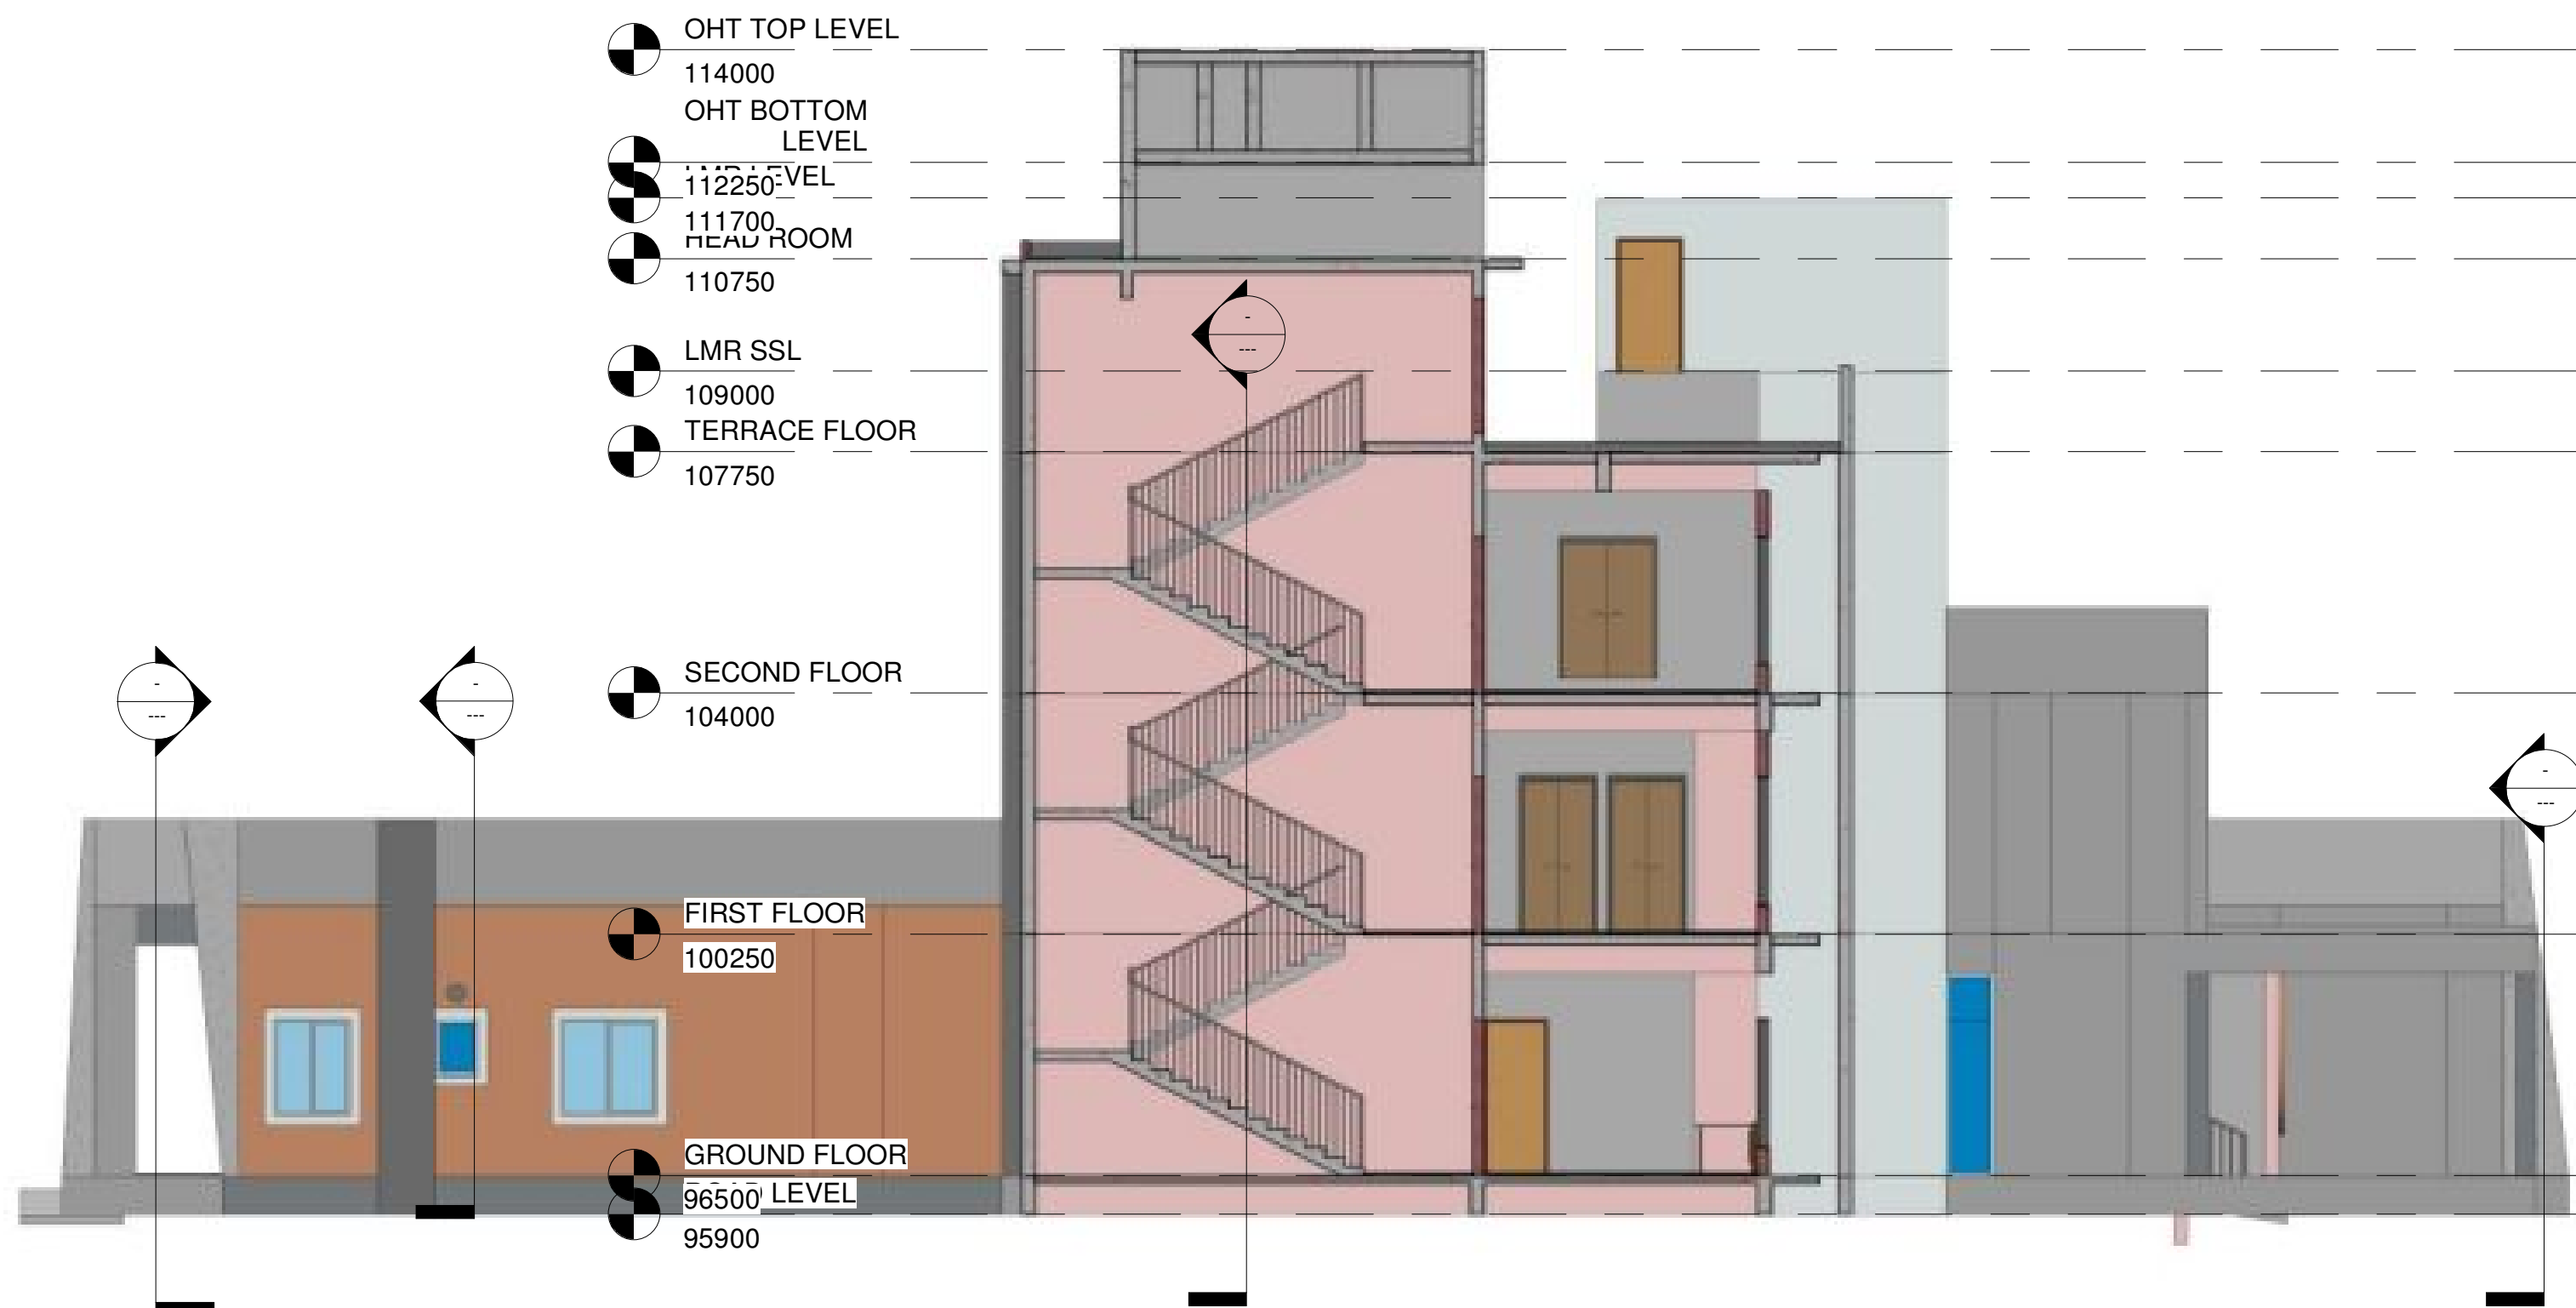

4 Section 18
1 : 100



3 {3D}

PROJECT : NSG CAMPUS

GENERAL NOTES :

1. ALL DIMENSIONS ARE IN MILLIMETER UNLESS STATED OTHERWISE.
2. NO DIMENSION IS TO BE SCALED OFF THE DRAWING.
3. THIS DRAWING TO BE READ IN CONJUNCTION WITH ALL RELEVANT THIS DRAWING TO BE READ IN CONJUNCTION WITH ALL RELEVANT.
4. ANY DISCREPANCY IN DRAWING TO BE BROUGHT TO THE NOTICE OF ARCHITECTS BEFORE COMMENCEMENT OF WORK.
5. FOR ALL STAIRS, ELEVATORS, TOILETS - REF SEPARATE DETAILS.
6. FOR ALL SERVICE DRAWINGS - REFER SEPARATE DETAILS.

KEY PLAN:



SIGNED/STAMPED BY :
BPR INFRASTRUCTURE PRIVATE LIMITED



SIGNED/STAMPED BY :
B DESIGN STUDIOS

ISSUE/REVISION

IR	DATE	DESCRIPTION

IR	DATE	DESCRIPTION
----	------	-------------

CLIENT
CPWD
CENTRAL PUBLIC WORKS DEPARTMENT

EPC CONTRACTOR
M/S BPR INFRASTRUCTURE PRIVATE LIMITED
Plot No. 103 & 104, 1st Floor Capital Park, Road, Madhavaram, Hyderabad, Telangana, 500011.

EPC ARCHITECT
B DESIGN STUDIOS
3rd Floor, ANR Gurni Square Plot No. 103, Road, Jalandhar, Madhavaram, Hyderabad, Telangana 500011.
Website: www.bdesignstudios.in
Phone: 080-88888888

EPC STRUCTURAL & MEP CONSULTANT
SUNV ENGINEERING SERVICES
Plot No. 103 & 104, 1st Floor Capital Park, Road, Madhavaram, Hyderabad, Telangana 500011.
Phone: 080-88888888

PROJECT :
Construction of NSG Regional Hub at Lekhawada, Gandhinagar, Gujarat.(SH - Construction of 104 nos Type-II, 40 nos Type-III, 14 nos Type-IV, 2 nos Type-V, 1 no. Administrative building cum Lecture hall, 1 no. Officers mess, 1 no. AC mess, 1 no. 280 men CDO barracks, 1 no. Quarter Guard, 1 no. MI Room cum Canteen cum Pre Primary School, 1 no. Electric substation, 1 no. STP, UG sump and 2 nos. Pump room including Internal Water Supply, Sanitary installation and Electrical work.External Service connection of Civil & Electrical, Internal roads, Cement Concrete pavement, Foot path, Storm water drains, Culverts, Retaining wall, etc. and all civil services and E & M services in Engineering, Procurement and Construction mode-I, Package-II).
Agreement No: 01/CE/EE/OGNR-II/2025-26

BLOCK : OFFICER'S MESS

DRAWING TITLE : STAIRCASE AND FLOOR PLAN, 3D

DESIGN : SATHYA APPROVED : RAJESH

SCALE : 1:75 DRAWN : B. MEGHANA

DATE : 16-04-2026 CHECKED : SATHYA

DRAWING NO : A102			
PROJECT NO :	SHEET SIZE :	CONSTRUCTION :	REVISION :
006	A1	C	R0