


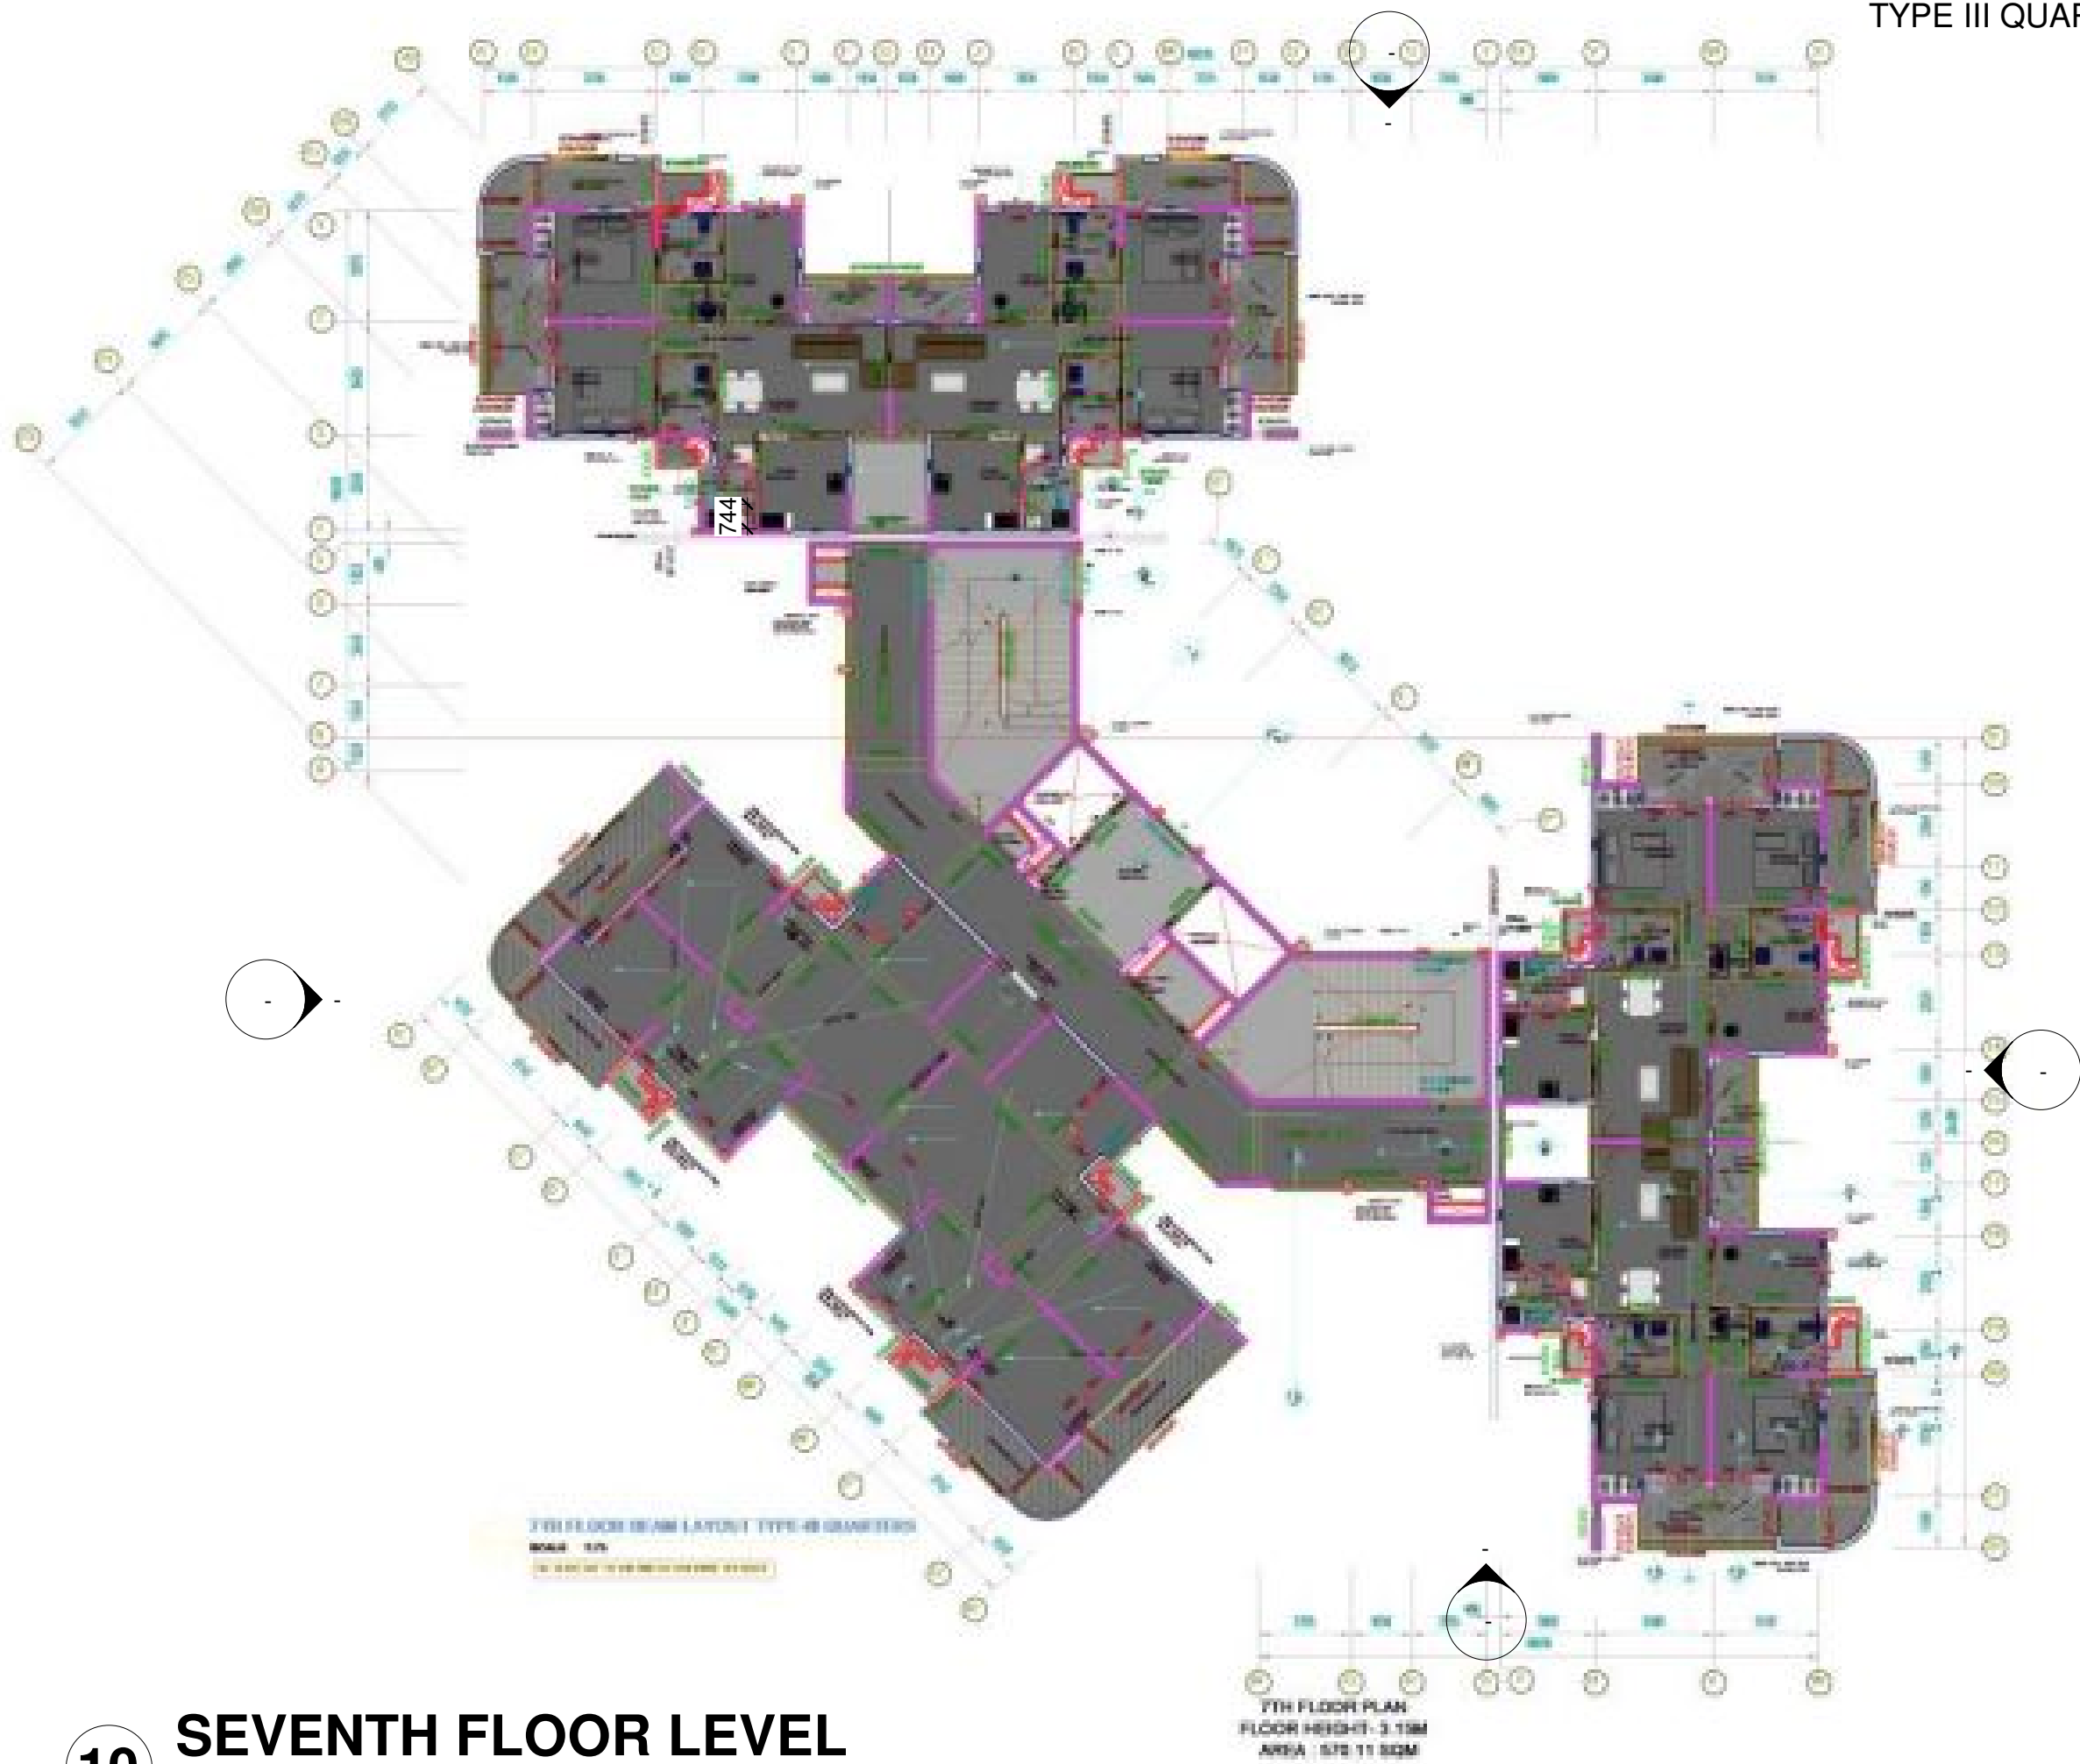


10 SEVENTH FLOOR LEVEL
1 : 200



11 TERRACE FLOOR LEVEL
1 : 200



12 HEAD ROOM LEVEL
1 : 250

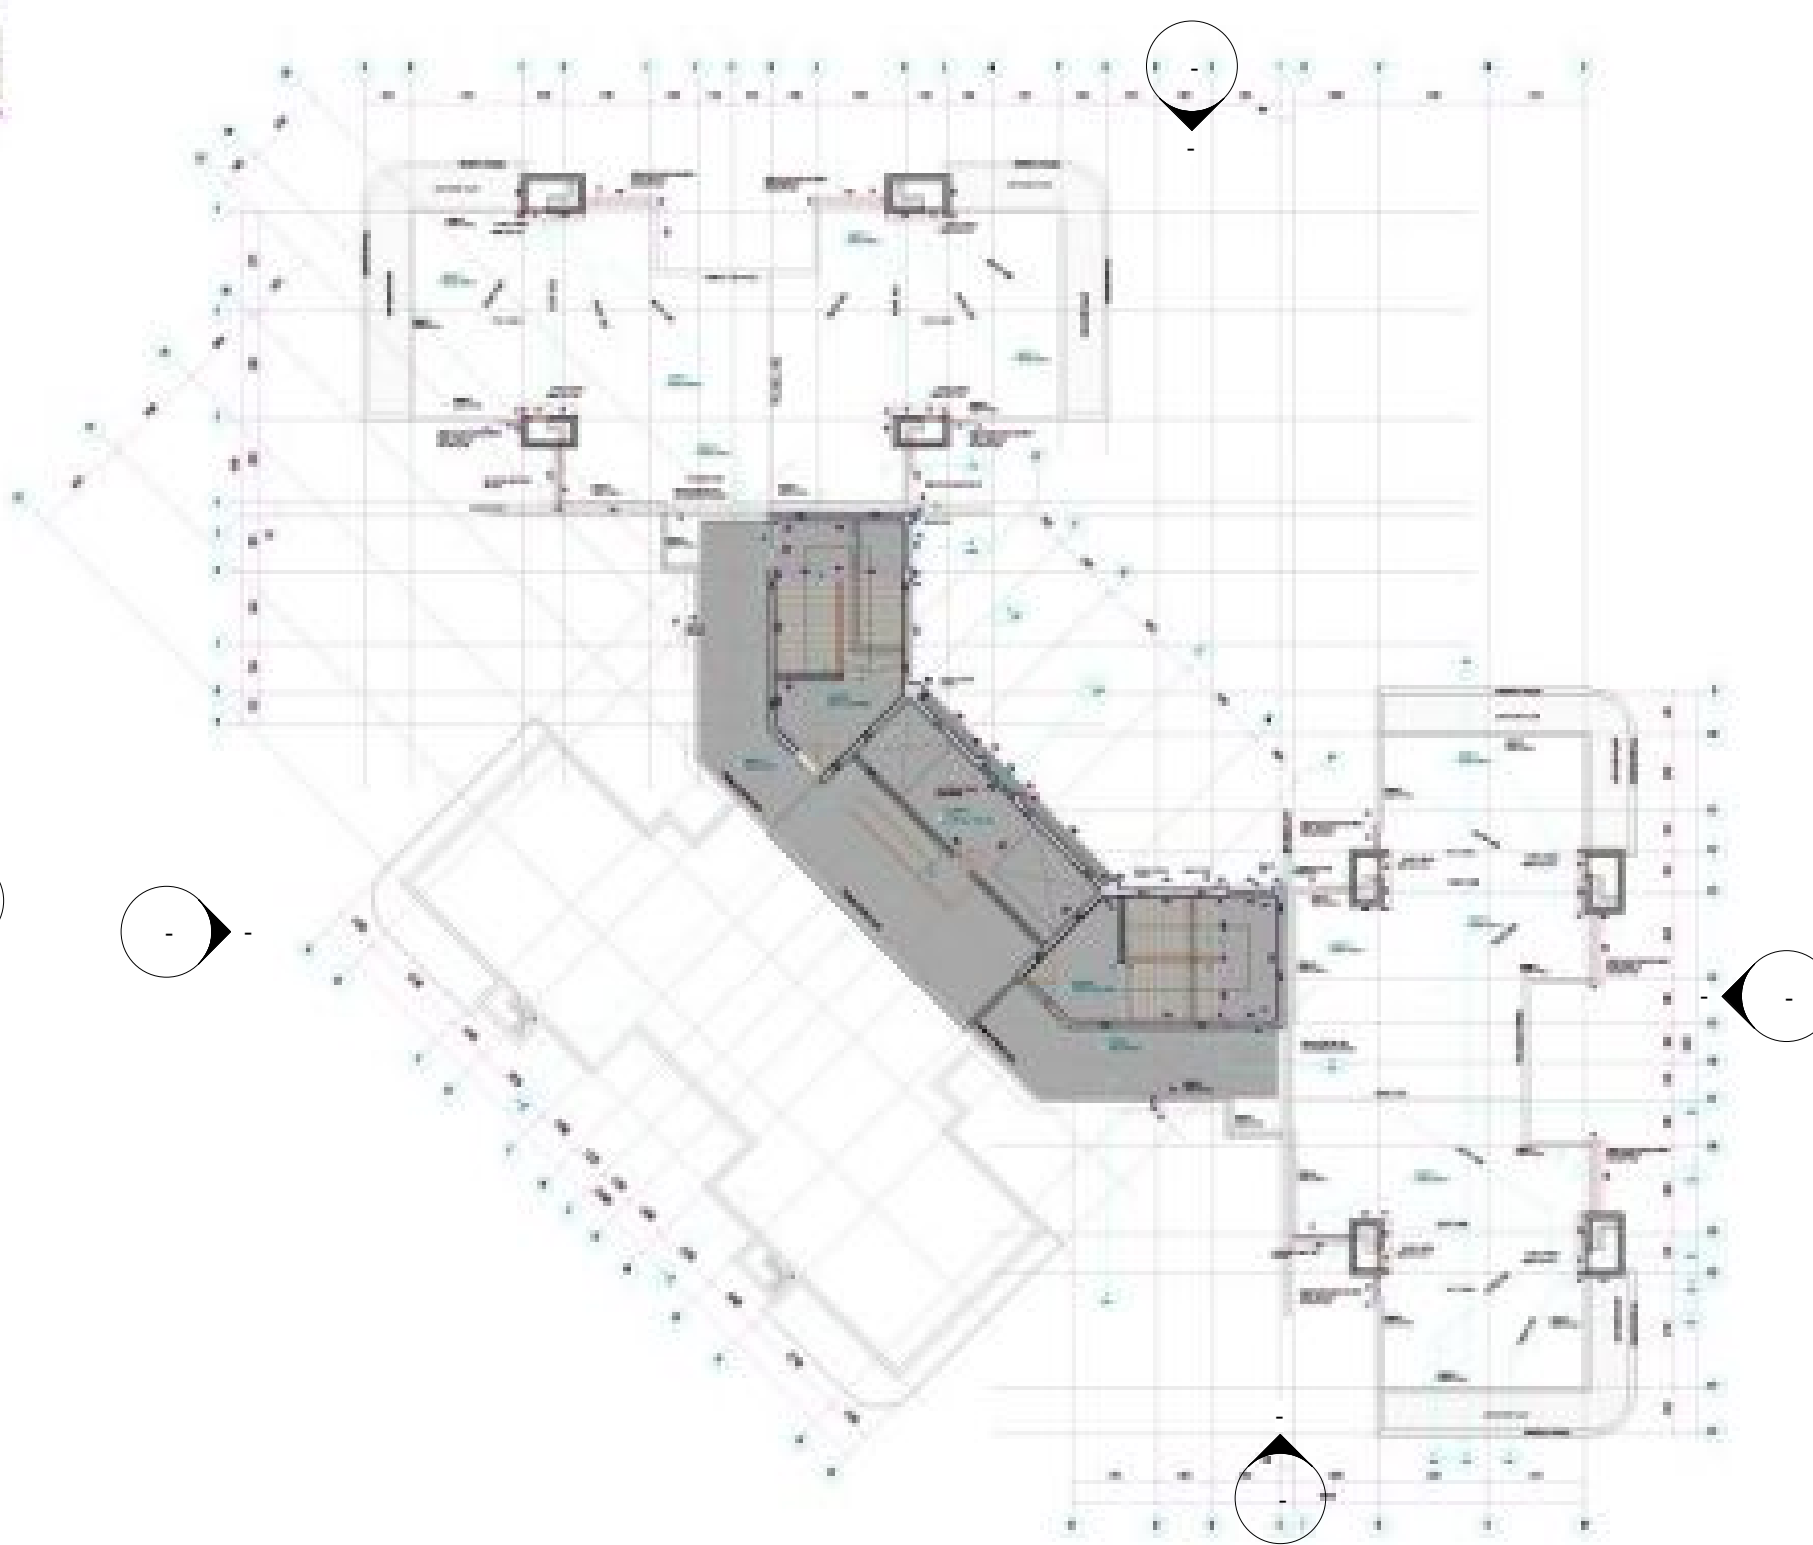

13 OHT BOTTOM LEVEL
1 : 250

TYPE III QUARTERS FLOORS PLANS AND LAYOUTS

PROJECT : NSG CAMPUS

GENERAL NOTES :

1. ALL DIMENSIONS ARE IN MILLIMETER UNLESS STATED OTHERWISE.
2. NO DIMENSION IS TO BE SCALED OFF THE DRAWING.
3. THIS DRAWING IS TO BE READ IN CONJUNCTION WITH ALL RELEVANT THIS DRAWING TO BE READ IN CONJUNCTION WITH ALL RELEVANT.
4. ANY DISCREPANCY IN DRAWING TO BE BROUGHT TO THE NOTICE OF ARCHITECTS BEFORE COMMENCEMENT OF WORK.
5. FOR ALL STAIRS, ELEVATORS, TOILETS - REF SEPARATE DETAILS.
6. FOR ALL SERVICE DRAWINGS - REFER SEPARATE DETAILS.

KEY PLAN:



SIGNED/STAMPED BY :
BPR INFRASTRUCTURE PRIVATE LIMITED



SIGNED/STAMPED BY :
B DESIGN STUDIOS

ISSUE/REVISION

IR	DATE	DESCRIPTION

CLIENT

CPWD
CENTRAL PUBLIC WORKS DEPARTMENT

EPC CONTRACTOR

M/S BPR INFRASTRUCTURE PRIVATE LIMITED
Plot No. 103 & 104, 1st Floor, Capital Park, Road, Madhavaram, Hyderabad, Telangana, 500081.

EPC ARCHITECT

B DESIGN STUDIOS
2nd Floor, 2nd Cross, Gandhi Nagar, Plot No. 103 & 104, 1st Floor, Capital Park, Road, Madhavaram, Hyderabad, Telangana, 500081.

EPC STRUCTURAL & MEP CONSULTANT

SUNV ENGINEERING SERVICES
PDR's N Square, Madhavaram, Hyderabad, Telangana, 500081. Phone: 922201 8440.

PROJECT :

Construction of NSG Regional Hub at Lekhawada, Gandhinagar, Gujarat (SH) - Construction of 104 nos Type-II, 40 nos Type-III, 14 nos Type-IV, 2 nos Type-V, 1 no. Administrative building cum Lecture hall, 1 no. Officers mess, 1 no. AC mess, 1 no. 280 men CDO barrack, 1 no. Quarter Guard, 1 no. M Room cum Canteen cum Pre Primary School, 1 no. Electric substation, 1 no. STP, UG sump and 2 nos. Pump room including Internal Water Supply, Sanitary installation and Electrical work.External Service connection of Civil & Electrical, Internal roads, Cement Concrete pavement, Foot path, Storm water drains, Culverts, Retaining wall, etc. and all civil services and E & M services in Engineering, Procurement and Construction mode-I, Package-II Agreement No: 01/CE/EE(O)GNR-II/2025-26

BLOCK : TYPE III QUARTERS

DRAWING TITLE : TYPE III QUARTERS FLOORS PLANS AND LAYOUTS

DESIGN : SATHYA APPROVED : RAJESH

SCALE : 1:75 DRAWN : B.MEGHANA

DATE : 16-04-2026 CHECKED : SATHYA

DRAWING NO : A105

PROJECT NO	SHEET SIZE	CONSTRUCTION	REVISION
006	A1	C	R0

