ELEVATIONS

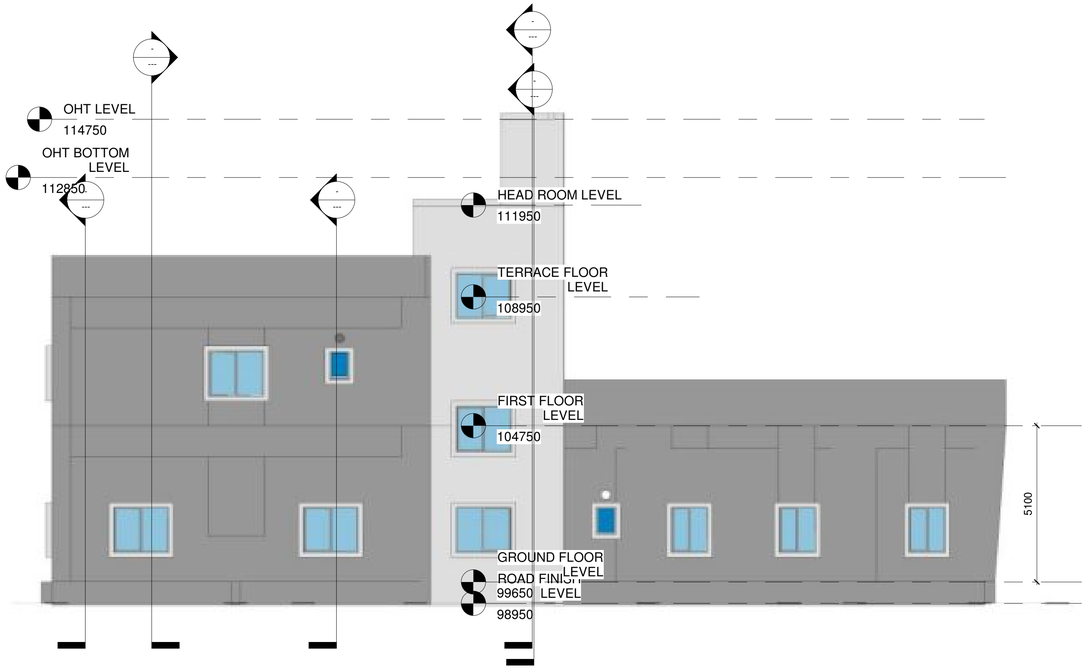

1 **North**
1 : 100

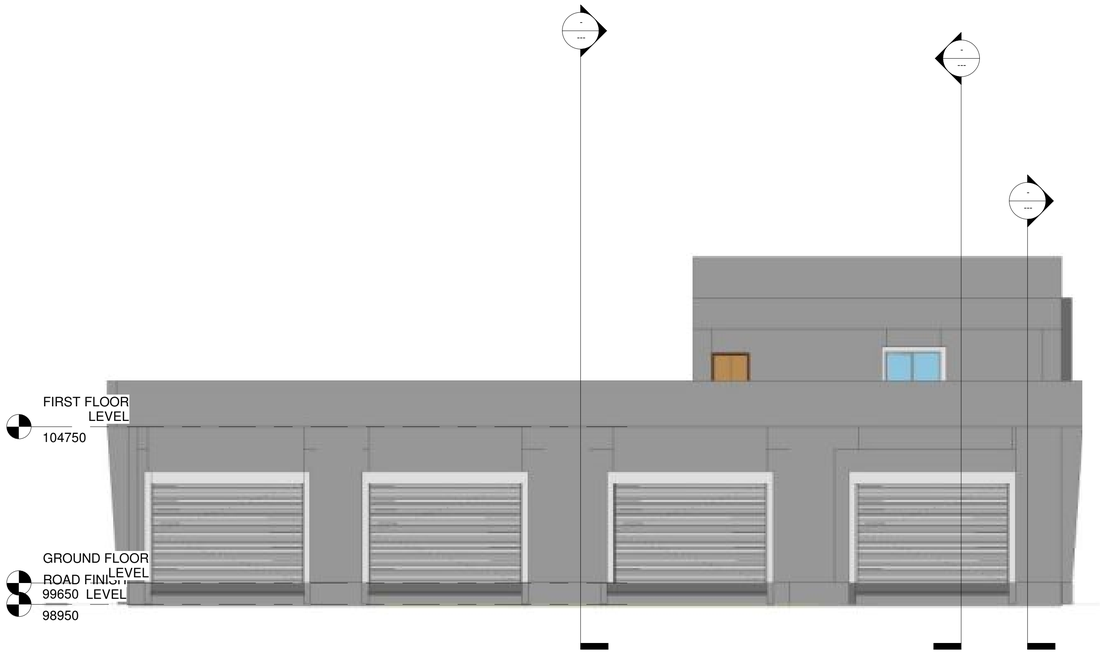

2 **South**
1 : 100

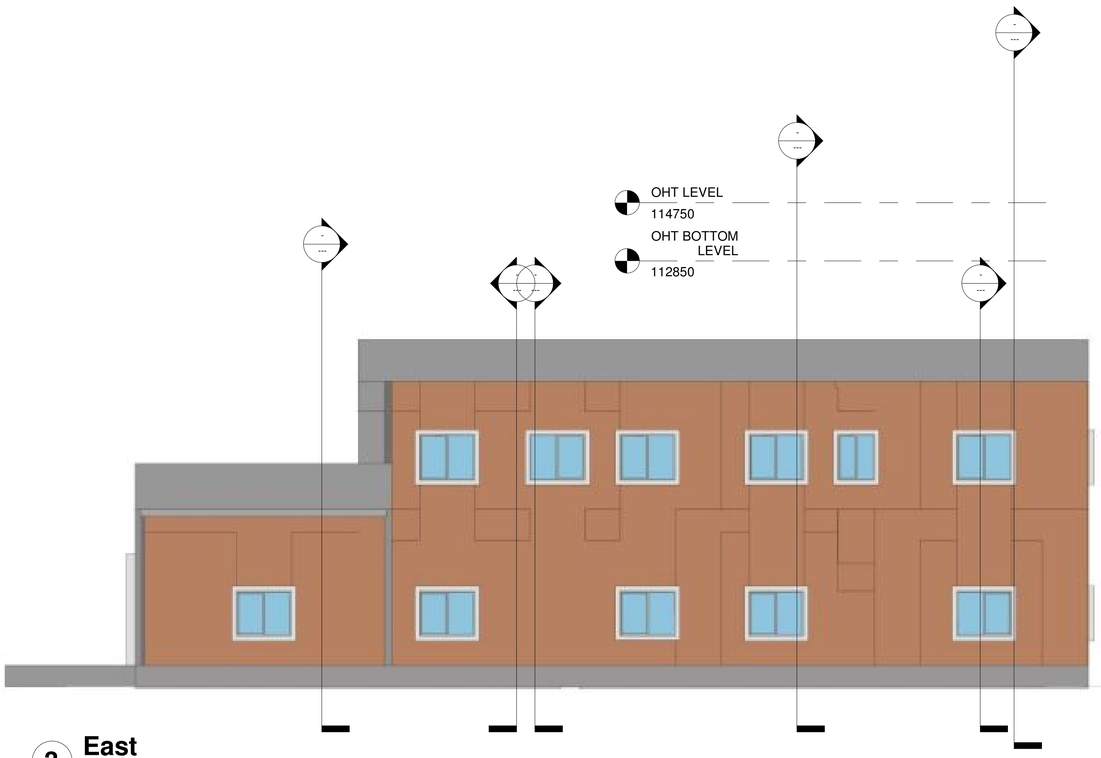

3 **East**
1 : 100

4 **West**
1 : 110

PROJECT : NSG CAMPUS

GENERAL NOTES :

1. ALL DIMENSIONS ARE IN MILLIMETER UNLESS STATED OTHERWISE.
2. NO DIMENSION IS TO BE SCALED OFF THE DRAWING.
3. THIS DRAWING TO BE READ IN CONJUNCTION WITH ALL RELEVANT THIS DRAWING TO BE READ IN CONJUNCTION WITH ALL RELEVANT.
4. ANY DISCREPANCY IN DRAWING, TO BE BROUGHT TO THE NOTICE OF ARCHITECTS BEFORE COMMENCEMENT OF WORK.
5. FOR ALL STAIRS, ELEVATORS, TOILETS -REF SEPARATE DETAILS.
6. FOR ALL SERVICE DRAWINGS - REFER SEPARATE DETAILS.

KEY PLAN:

SIGNED/STAMPED BY :
BPR INFRASTRUCTURE PRIVATE LIMITED

SIGNED/STAMPED BY :
B DESIGN STUDIOS

ISSUE/REVISION

I/R	DATE	DESCRIPTION

CLIENT
CPWD
CENTRAL PUBLIC WORKS DEPARTMENT

EPC CONTRACTOR
M/S BPR INFRASTRUCTURE PRIVATE LIMITED
Plot No. 8,9,10,11, Silicon valley Layout, Flat no. 103 & 104, 1st Floor Capital Park Road , Madhapur , Hyderabad, Telangana - 500081.

EPC ARCHITECT
B DESIGN STUDIOS
3rd Floor, KNR Gamut Square Plot No. 2/8,
100 Road, Jahind Enclave, Madhapur, Hyderabad, Telangana 500081.
website: info@bdesignstudios.in
Ph.no: +91-40-48577181

EPC STRUCTURAL & MEP CONSULTANT
SUVIH ENGINEERING SERVICES
PSR's N Square, Madhapur, Hyderabad,
Telangana 500081
Phone: 073307 56745

PROJECT :
Construction of NSG Regional Hub at Lekhawada, Gandhinagar, Gujarat.(SH :- Construction of 104 nos
Type-II, 40 nos Type-III, 14 nos Type-IV, 2 nos Type-V,
1 no. Administrative building cum Lecture hall, 1 no. Officers mess, 1 no. AC mess, 1 no. 280 men CDO barrack, 1 no. Quarter Guard, 1 no MI Room cum Canteen cum Pre Primary School, 1 no. Electric substation, 1 no. STP, UG sump and 2 nos. Pump room
including Internal Water Supply, Sanitary installation and Electrical work,External Service connection of Civil
& Electrical, Internal roads, Cement Concrete pavement, Foot path. Storm water drains, Culverts, Retaining wall, etc. and all civil services and E & M services in Engineering, Procurement and Construction
mode-I, Package-II).
Agreement No: 01/CE/EE(C)GNR-II/2025-26

BLOCK : ELECTRICAL SUBSTAION

DRAWING TITLE : ELEVATIONS

DESIGN : SATHYA	APPROVED : RAJESH
SCALE : 1:75	DRAWN :B.MEGHANA
DATE : 16-04-2026	CHECKED : SATHYA

DRAWING NO : A101

PROJECT NO.	SHEET SIZE	CONSTRUCTION	REVISION
006	A1	C	R0