



ELECTRICAL SUBSTATION FLOORS




1 {3D - Revit-3}

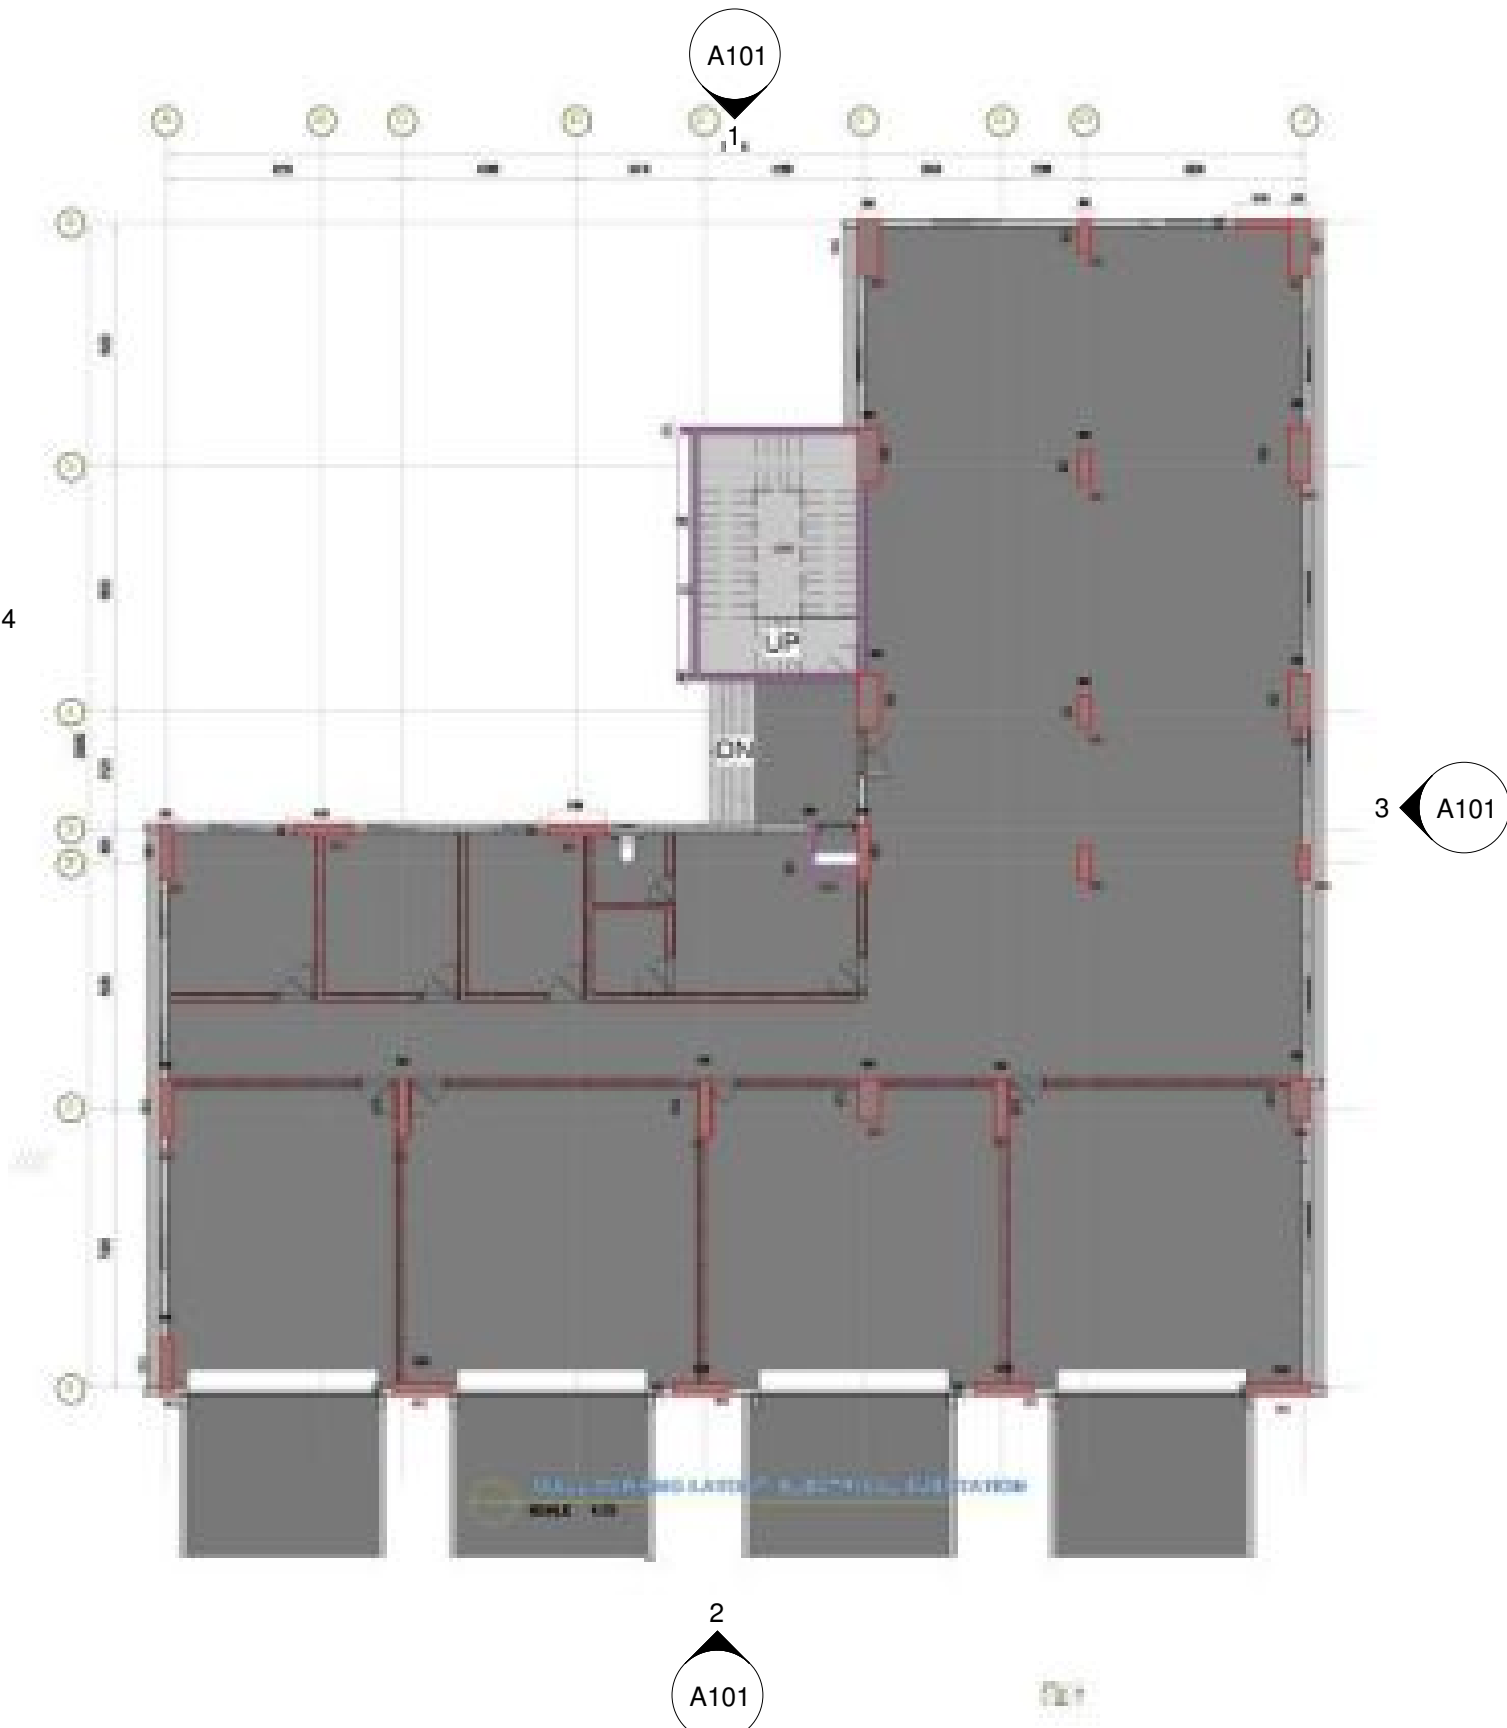

2 ROAD FINISH LEVEL
1 : 200

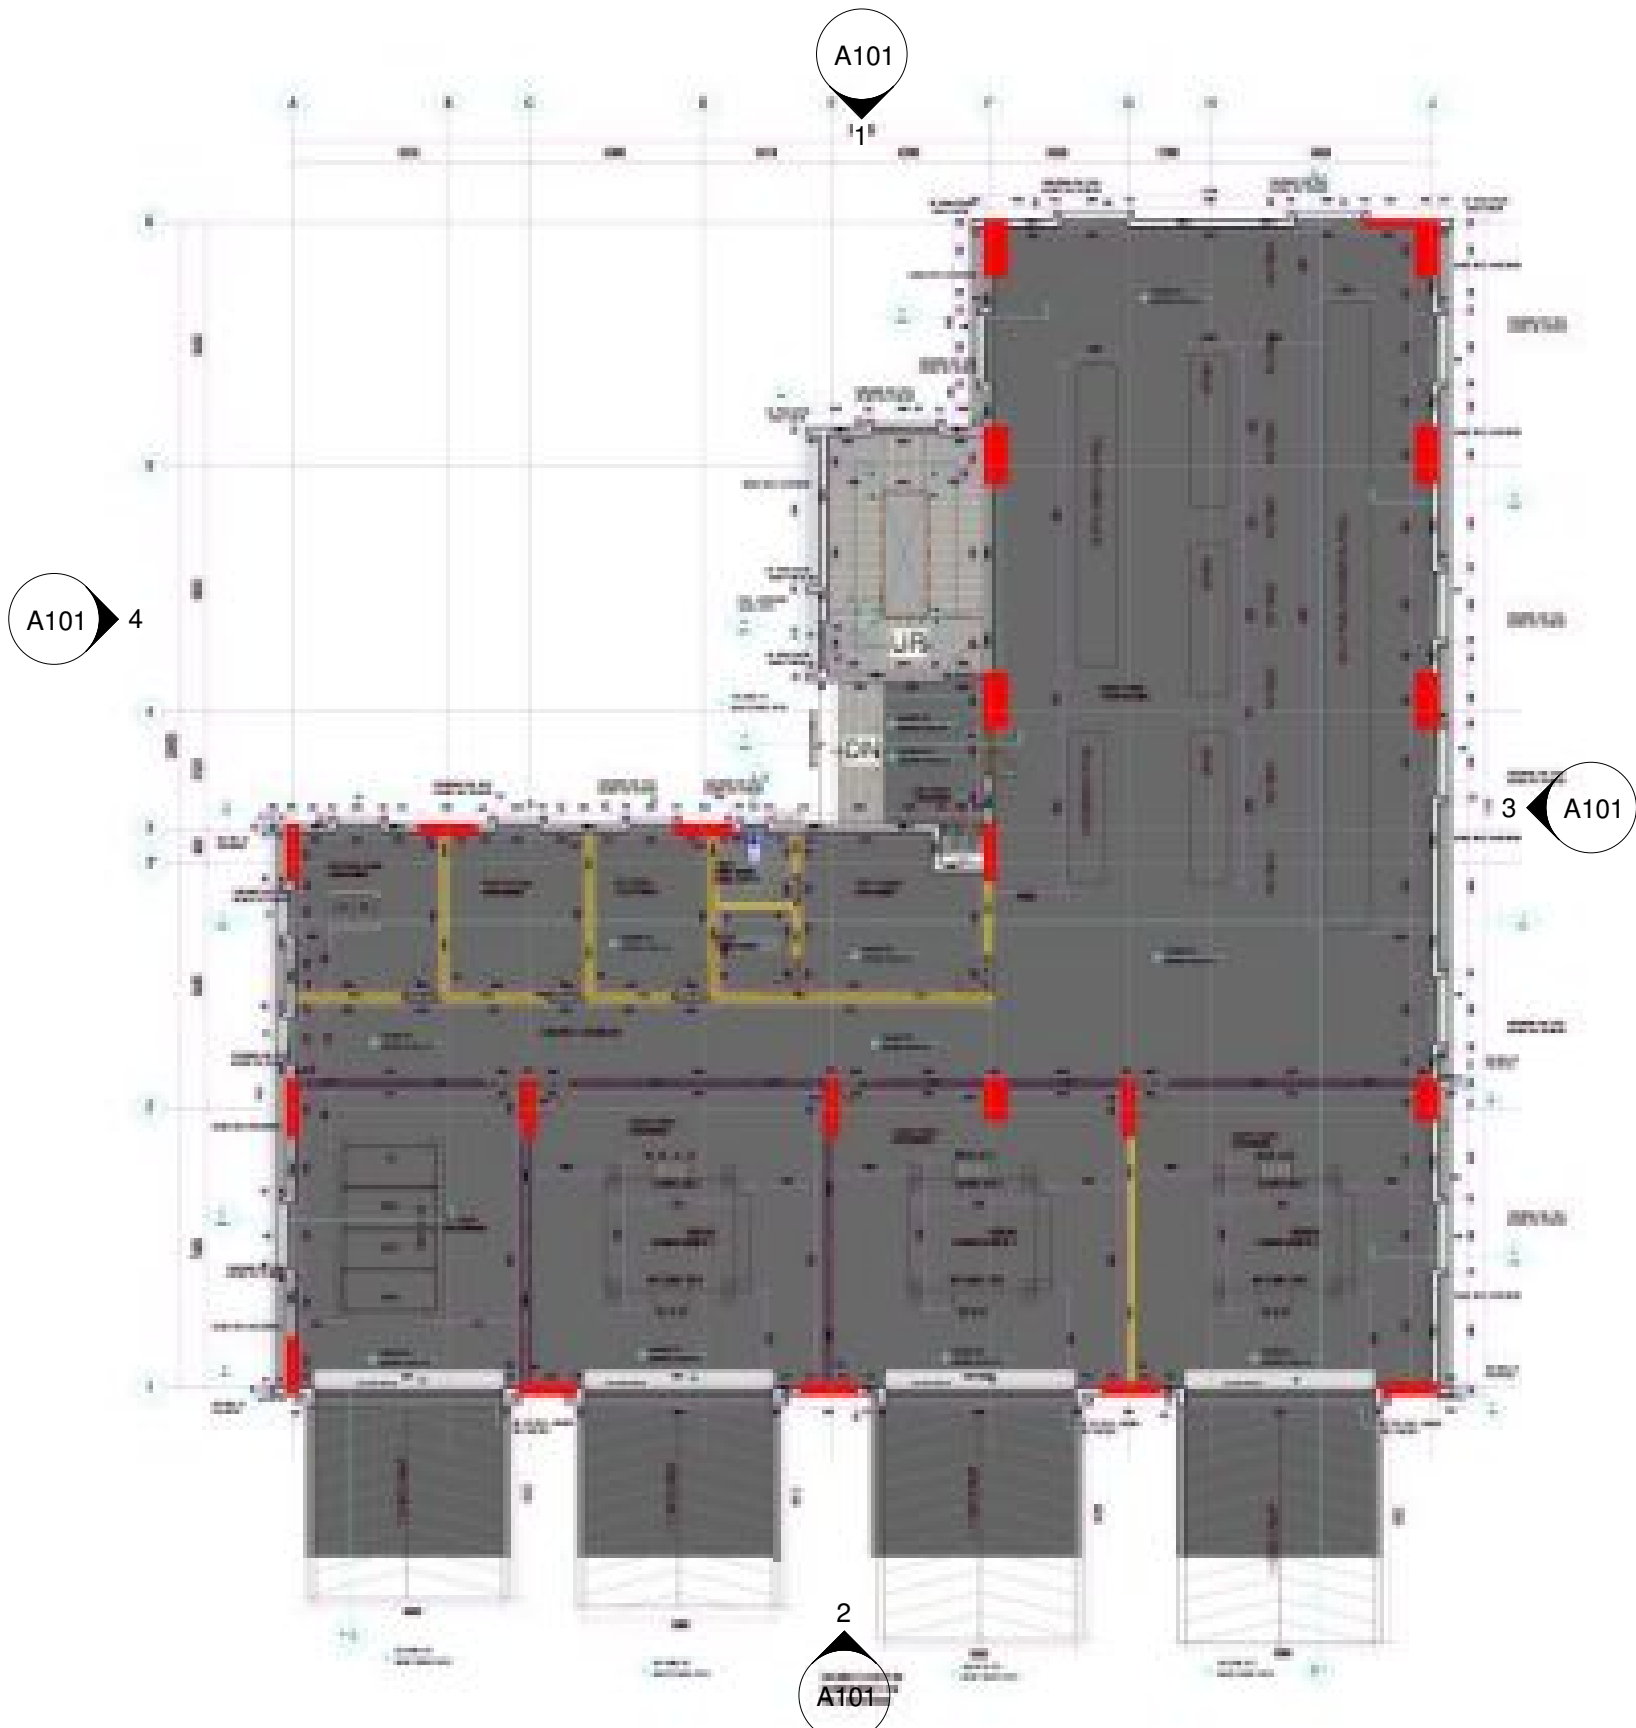


3 GROUND FLOOR LEVEL
1 : 200

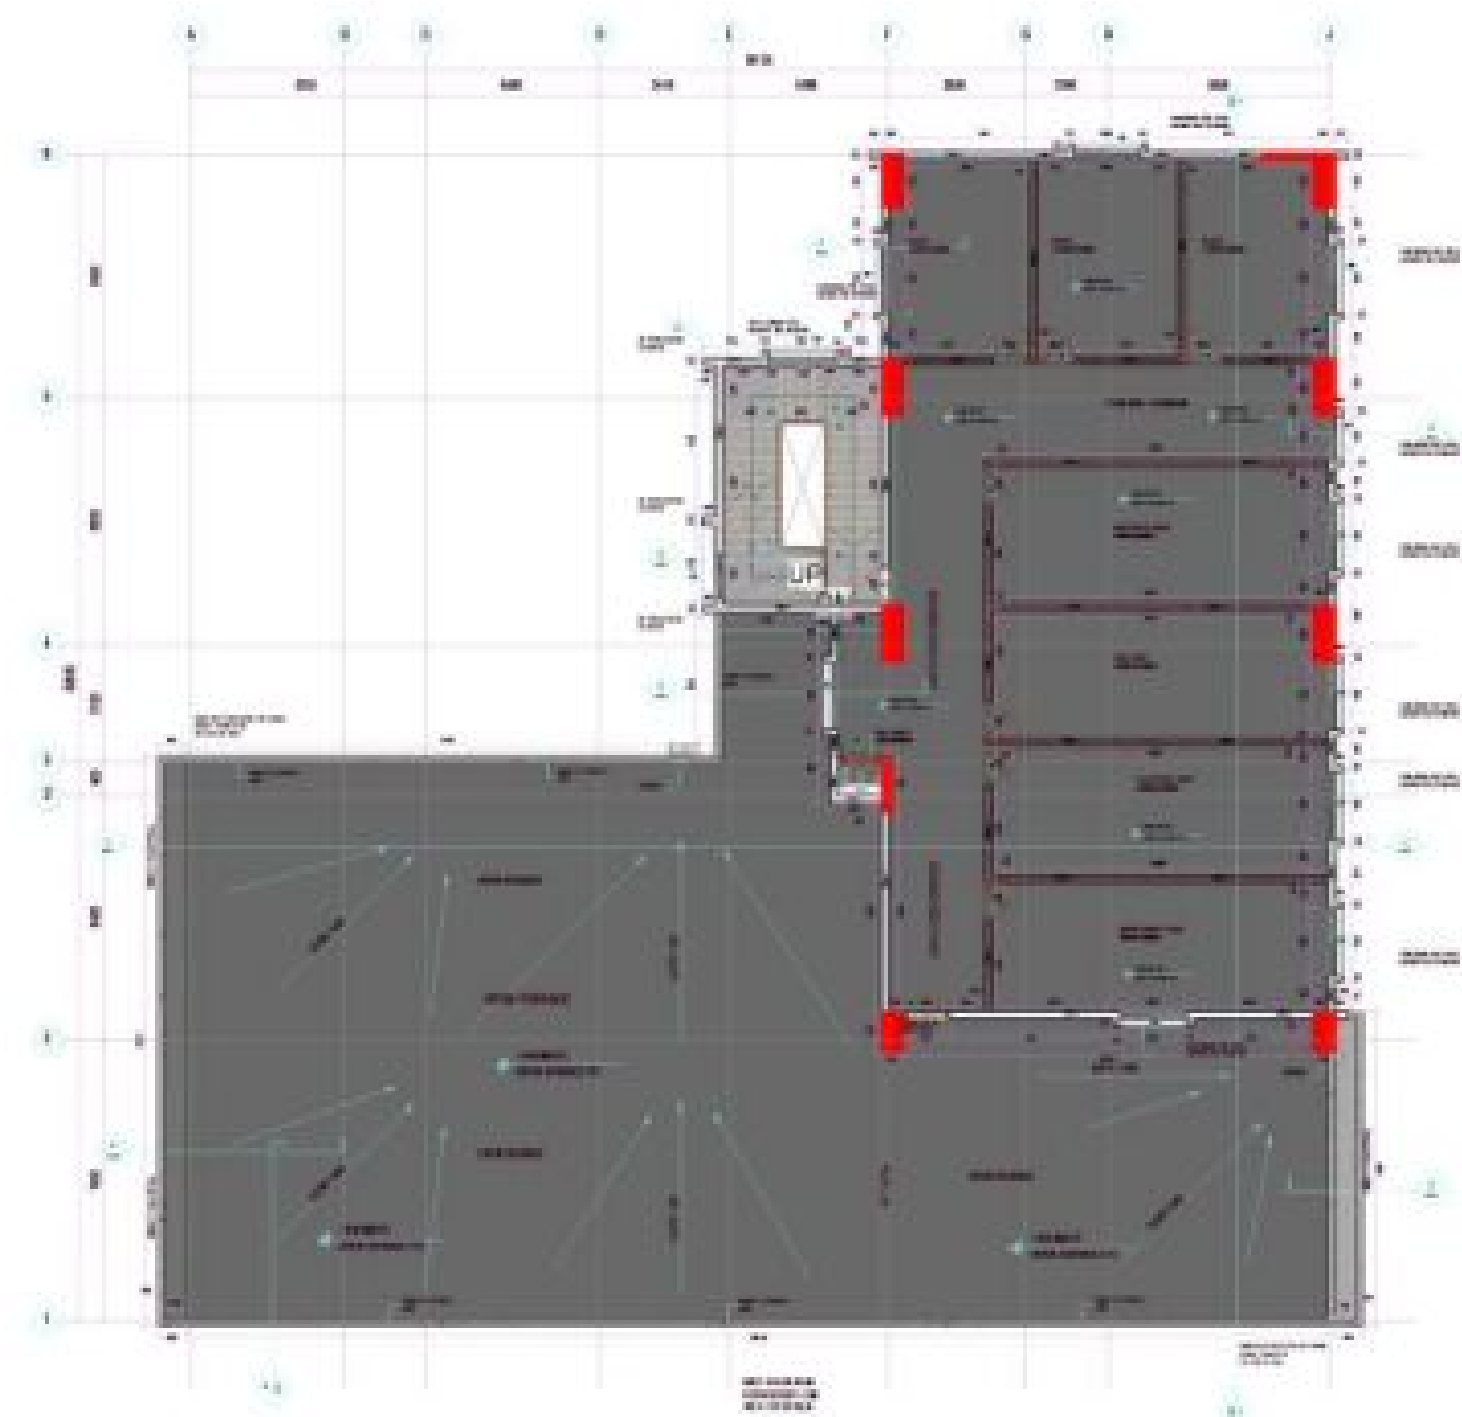

6 FIRST FLOOR LEVEL
1 : 200



7 TERRACE FLOOR LEVEL
1 : 200

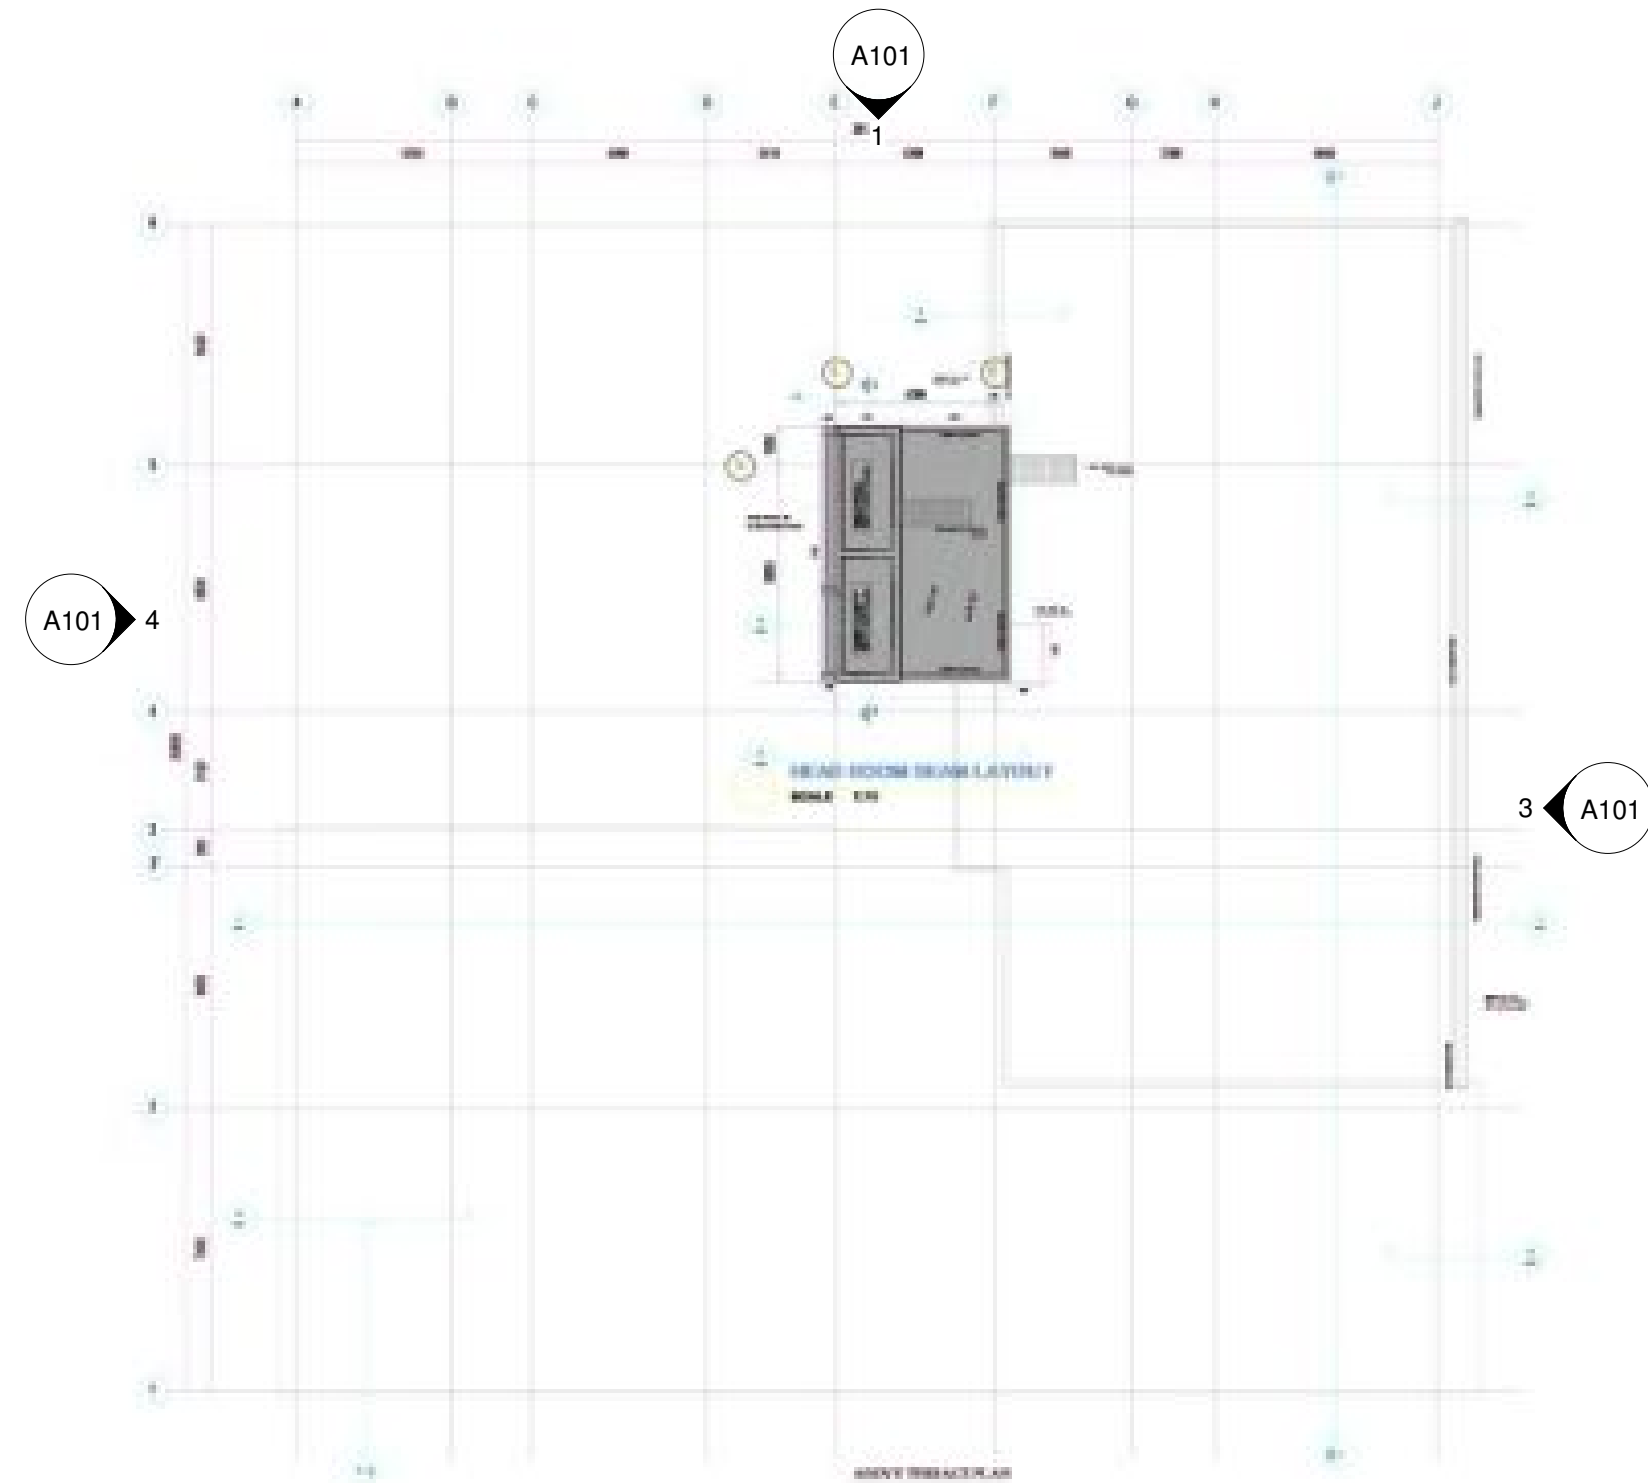

4 HEAD ROOM LEVEL
1 : 200

PROJECT : NSG CAMPUS

GENERAL NOTES :
1. ALL DIMENSIONS ARE IN MILLIMETER UNLESS STATED OTHERWISE.
2. NO DIMENSION IS TO BE SCALED OFF THE DRAWING.
3. THIS DRAWING TO BE READ IN CONJUNCTION WITH ALL RELEVANT THIS DRAWING TO BE READ IN CONJUNCTION WITH ALL RELEVANT
4. ANY DISCREPANCY IN DRAWING TO BE BROUGHT TO THE NOTICE OF ARCHITECTS BEFORE COMMENCEMENT OF WORK.
5. FOR ALL STAIRS, ELEVATORS, TOILETS - REF SEPARATE DETAILS.
6. FOR ALL SERVICE DRAWINGS - REFER SEPARATE DETAILS.

KEY PLAN:

SIGNED/STAMPED BY :
BPR INFRASTRUCTURE PRIVATE LIMITED

SIGNED/STAMPED BY :
B DESIGN STUDIOS

ISSUE/REVISION	DATE	DESCRIPTION

CLIENT
CPWD
CENTRAL PUBLIC WORKS DEPARTMENT

EPC CONTRACTOR

BPR INFRASTRUCTURE PRIVATE LIMITED
Plot No. 103 & 104, 1st Floor, Capital Park, Road, Madhapur, Hyderabad, Telangana, 500081.

EPC ARCHITECT

B DESIGN STUDIOS
2nd Floor, ARIH Grand Tower, Plot No. 103, Road, Madhapur, Hyderabad, Telangana 500081.
Website: www.bdesignstudios.in
Phone: 920201 8490

EPC STRUCTURAL & MEP CONSULTANT

SUVIM ENGINEERING SERVICES
PDR N Square, Madhapur, Hyderabad, Telangana 500081
Phone: 920201 8490

PROJECT :
Construction of NSG Regional Hub at Lekhawada, Gandhinagar, Gujarat (SH - Construction of 104 nos Type-II, 40 nos Type-III, 14 nos Type-IV, 2 nos Type-V, 1 no. Administrative building cum Lecture hall, 1 no. Officers mess, 1 no. AC mess, 1 no. 280 men CDO barrack, 1 no. Quarter Guard, 1 no. MI Room cum Canteen cum Pre Primary School, 1 no. Electric substation, 1 no. STP, UG sump and 2 nos. Pump room including Internal Water Supply, Sanitary installation and Electrical work, External Service connection of Civil & Electrical, Internal roads, Cement Concrete pavement, Foot path, Storm water drains, Culverts, Retaining wall, etc. and all civil services and E & M services in Engineering, Procurement and Construction mode-I, Package-II)
Agreement No: 01/CEE/OGNR-II/2025-26

BLOCK : ELECTRICAL SUBSTATION

DRAWING TITLE : FLOOR PLAN

DESIGN : SATHYA APPROVED : RAJESH

SCALE : 1:75 DRAWN : B.MEGHANA

DATE : 16-04-2026 CHECKED : SATHYA

DRAWING NO : A100

PROJECT NO	SHEET SIZE	CONSTRUCTION	REVISION
006	A1	C	R0