

GENERAL NOTES :

1. ALL DIMENSIONS ARE IN MILLIMETER UNLESS STATED OTHERWISE.
2. NO DIMENSION IS TO BE SCALED OFF THE DRAWING.
3. THIS DRAWING TO BE READ IN CONJUNCTION WITH ALL RELEVANT THIS DRAWING TO BE READ IN CONJUNCTION WITH ALL RELEVANT.
4. ANY DISCREPANCY IN DRAWING, TO BE BROUGHT TO THE NOTICE OF ARCHITECTS BEFORE COMMENCEMENT OF WORK.
5. FOR ALL STAIRS, ELEVATORS, TOILETS - REF SEPARATE DETAILS.
6. FOR ALL SERVICE DRAWINGS - REFER SEPARATE DETAILS.

KEY PLAN:




ISSUE/REVISION

I/R	DATE	DESCRIPTION
-----	------	-------------

CLIENT

CPWD
CENTRAL PUBLIC WORKS DEPARTMENT


EPC CONTRACTOR

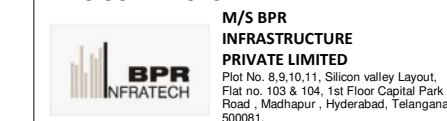

EPC ARCHITECT



EPC STRUCTURAL & MEP CONSULTANT

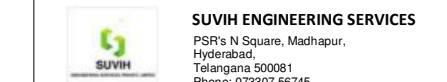

PROJECT :

Construction of NSG Regional Hub at Lekhavadh
Gandhinagar, Gujarat, (SIH : Construction of 104
nos
Type-II, 40 nos Type-III, 14 nos Type-IV, 2 nos Type-
V)
1 no. Administrative building cum Lecture hall, 1
Officers mess, 1 no. AC mess, 1 no. 280 cm CD
Kitchen, 1 no. Quarters, 1 no. 200 cm CD Kitchen,
Canteen cum Pre Primary School, 1 no. Electric
Substation, 1 no. STP, UO pump and 2 nos. Pump
room
including Internal Water Supply, Sanitary installation
and Electrical work, External Service connection of
Civil
& Electrical, Internal roads, Cement Concrete
Retaining wall, Foot path, Storm water drains, Culvert,
Retaining wall, etc. and all civil services and E & M
services in Engineering, Procurement and
Construction
mode-I Package-1)
Agreement No: 01/CEE/C(PGR-18/2025-26)

BLOCK	:	ELECTRICAL SUBSTATION
-------	---	-----------------------

DRAWING TITLE :	ESS 3D MODEL AND STAIRCASE
-----------------	----------------------------


DESIGN : SATHYA	APPROVED : RA
-----------------	---------------

SCALE : 1:75	DRAWN :B.ME
--------------	-------------


DATE : 16-04-2026	CHECKED : SA
-------------------	--------------

DRAWING NO : A102


PROJECT NO.	SHEET SIZE	CONSTRUCTION	REVISION
006	A1	C	R0

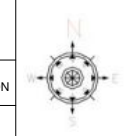

ESS 3D MODEL

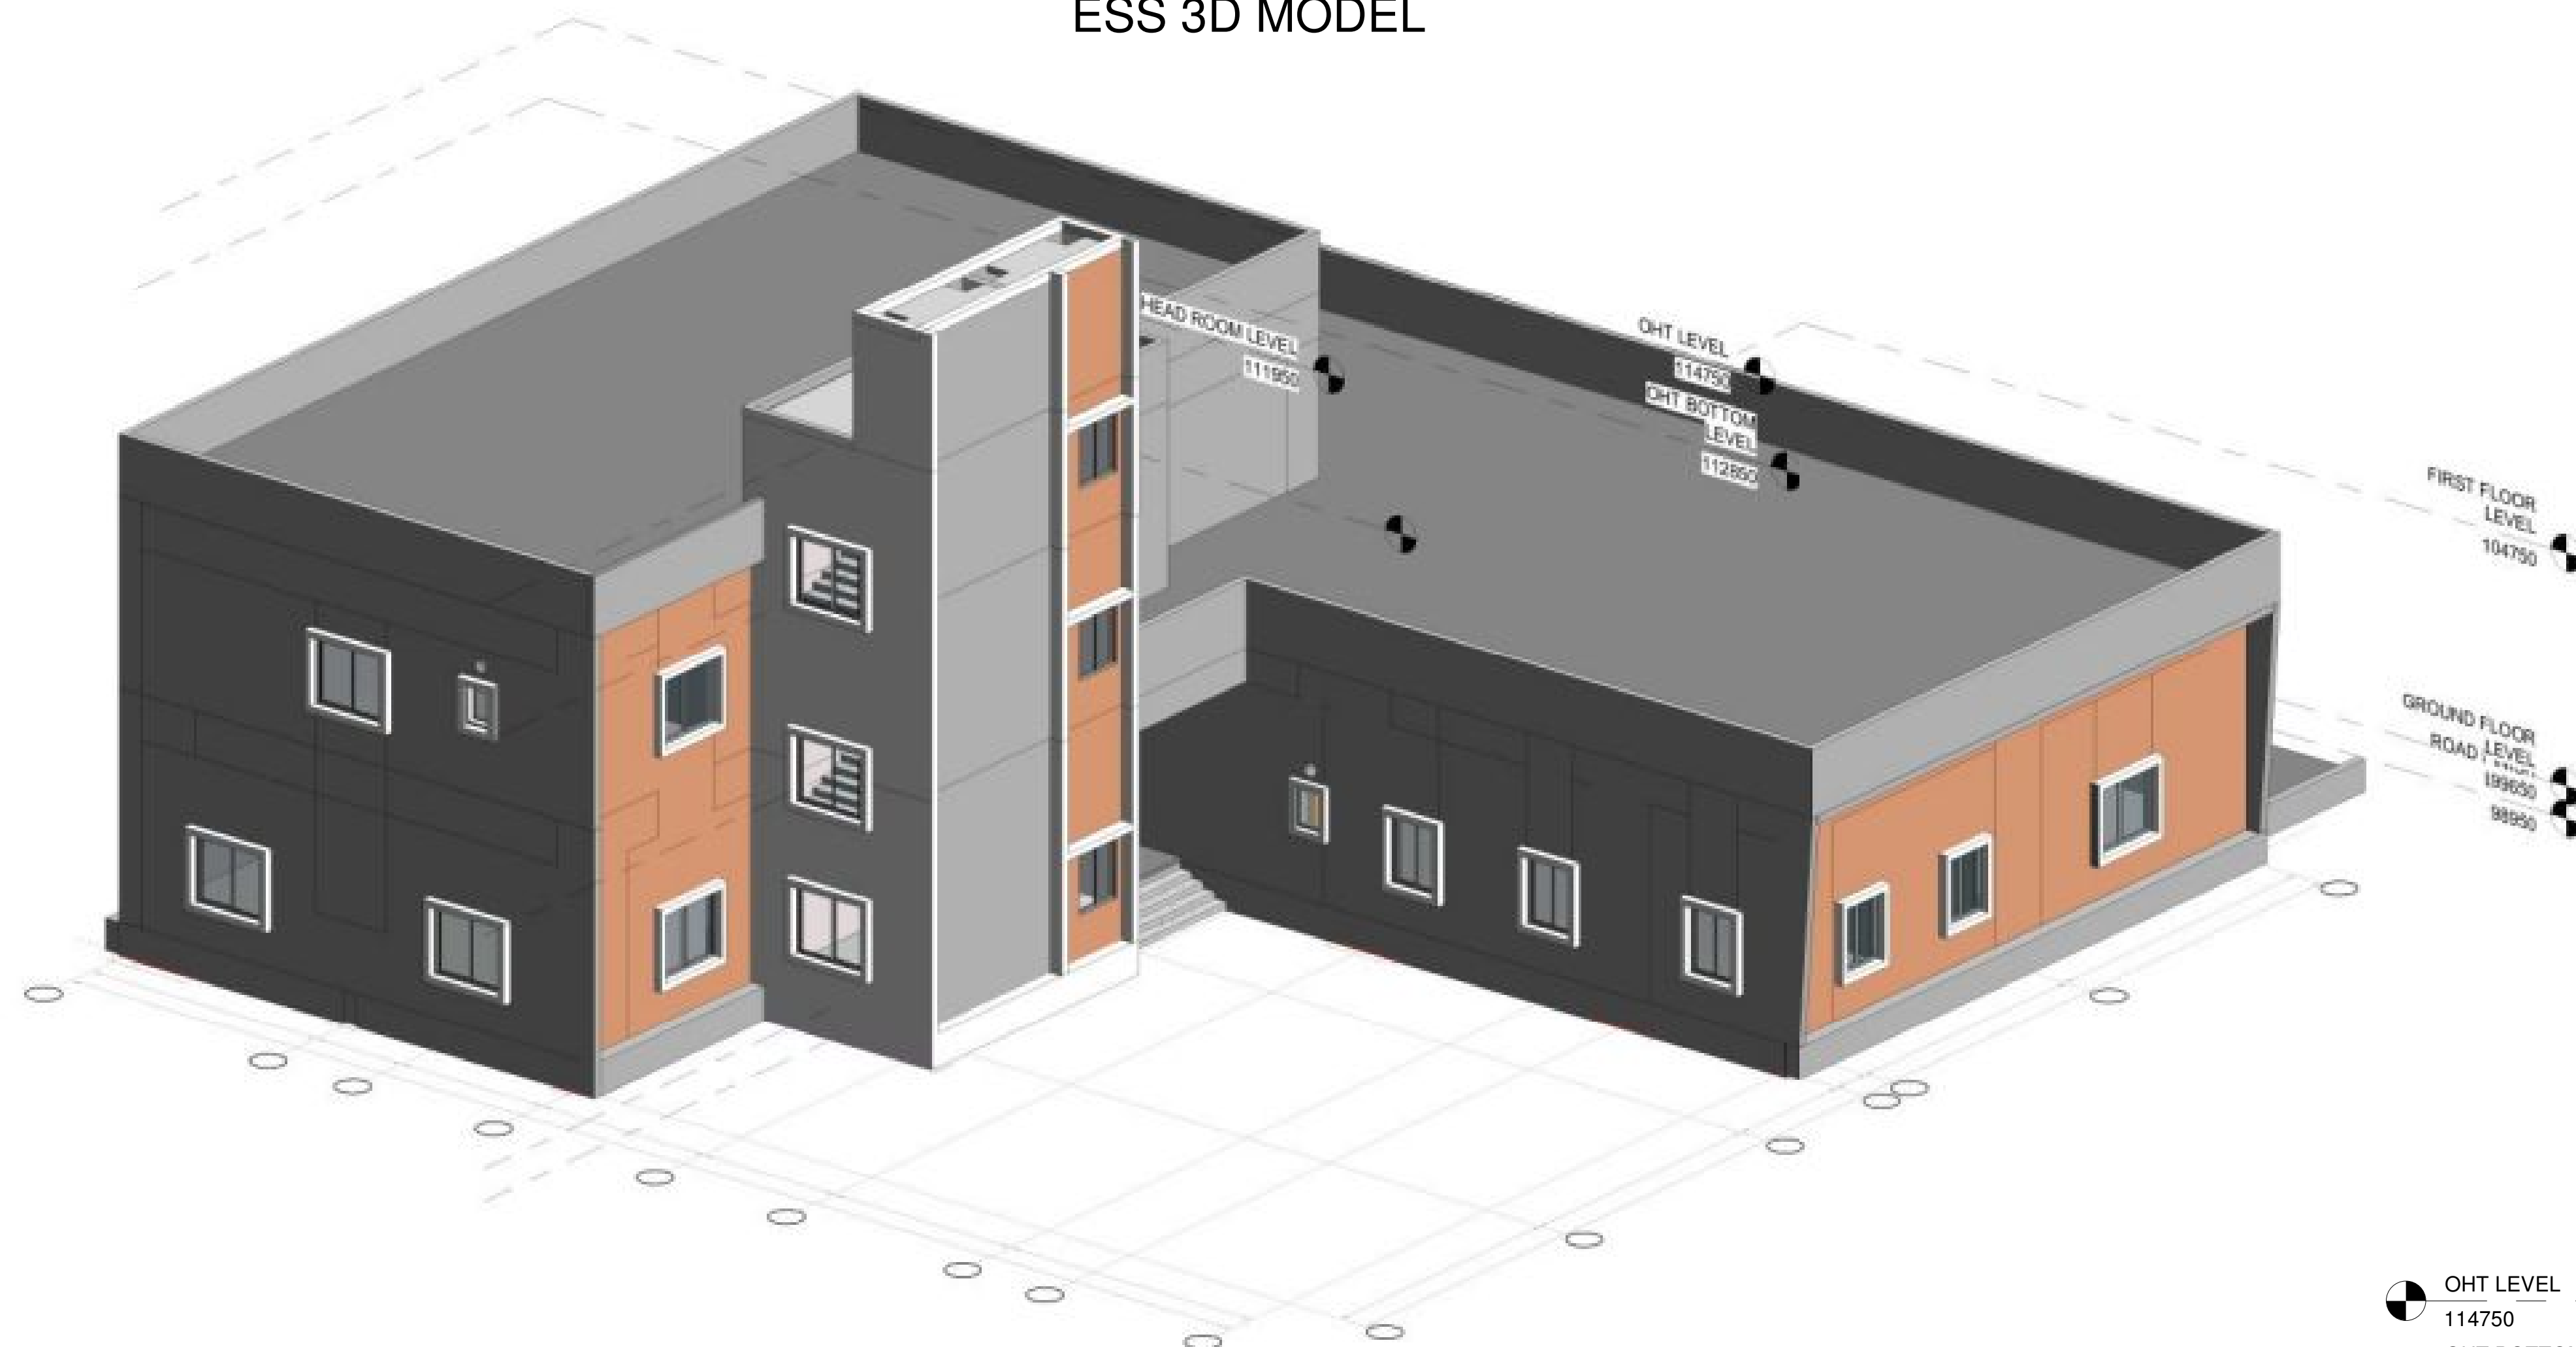

STAIRCASE

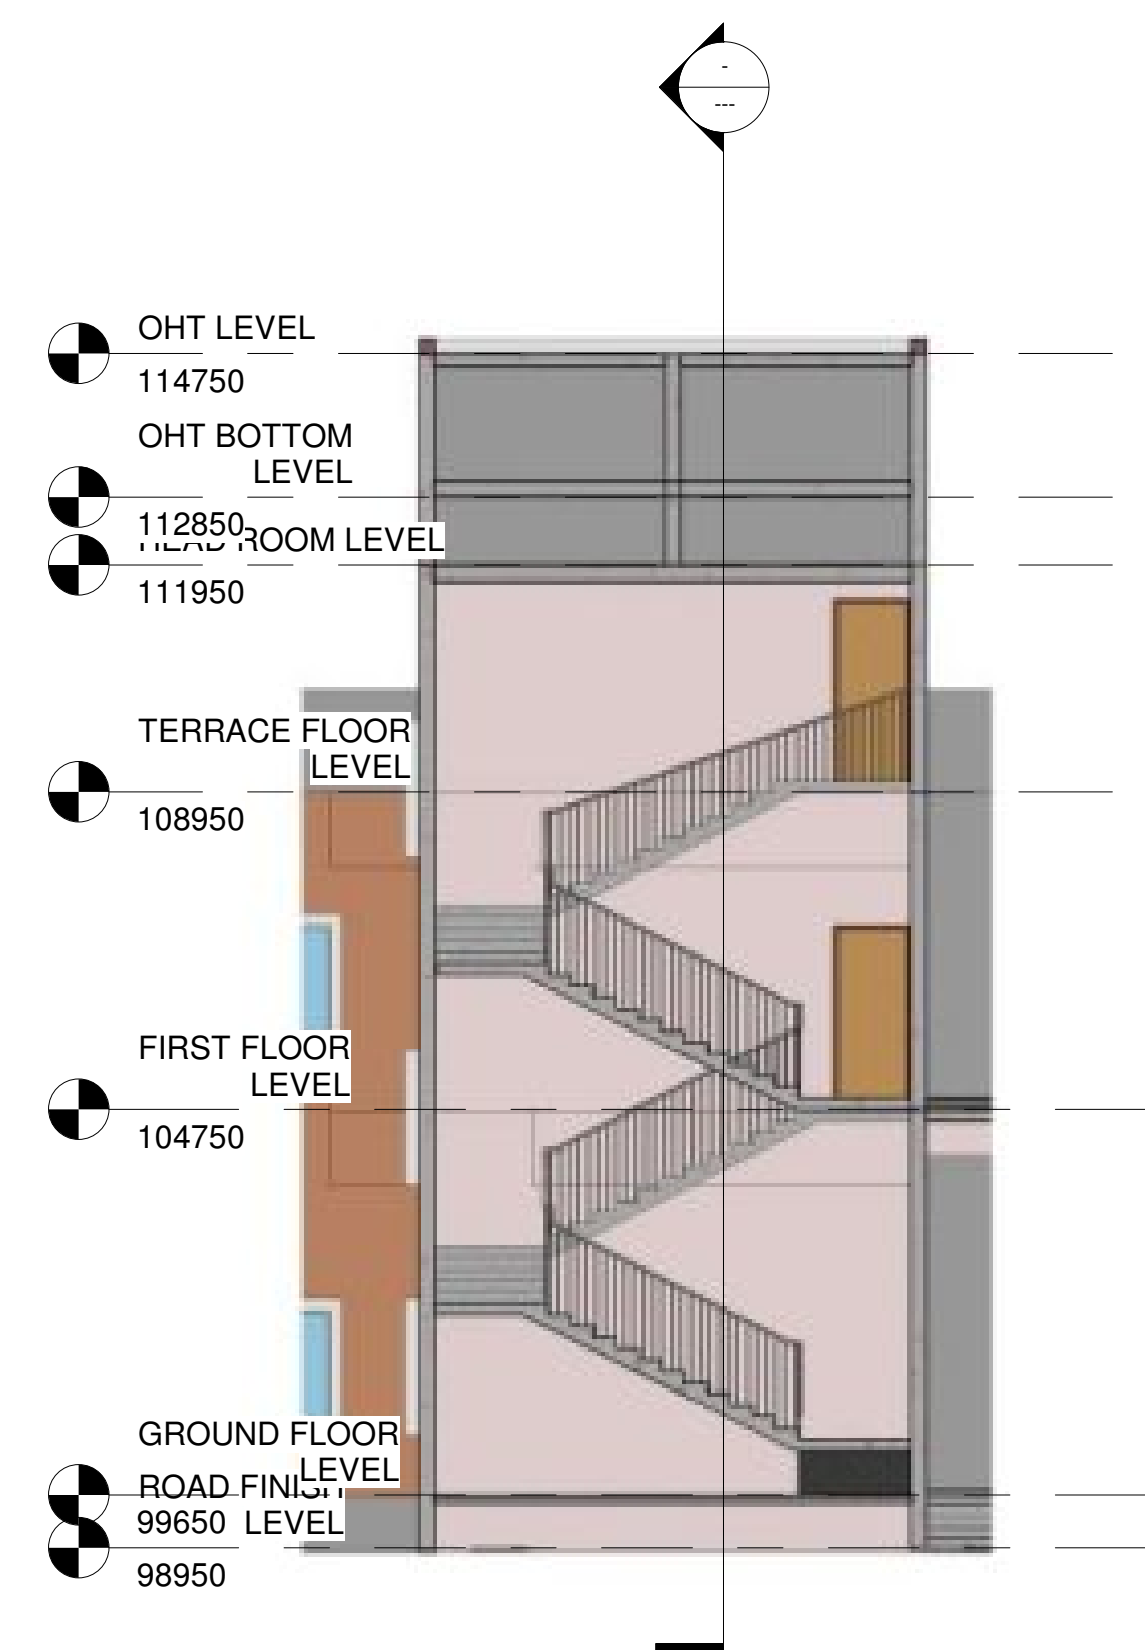

1 {3D - Revit-4}

2 **Section 6**
1 : 100