



MI CSD ELEVATIONS

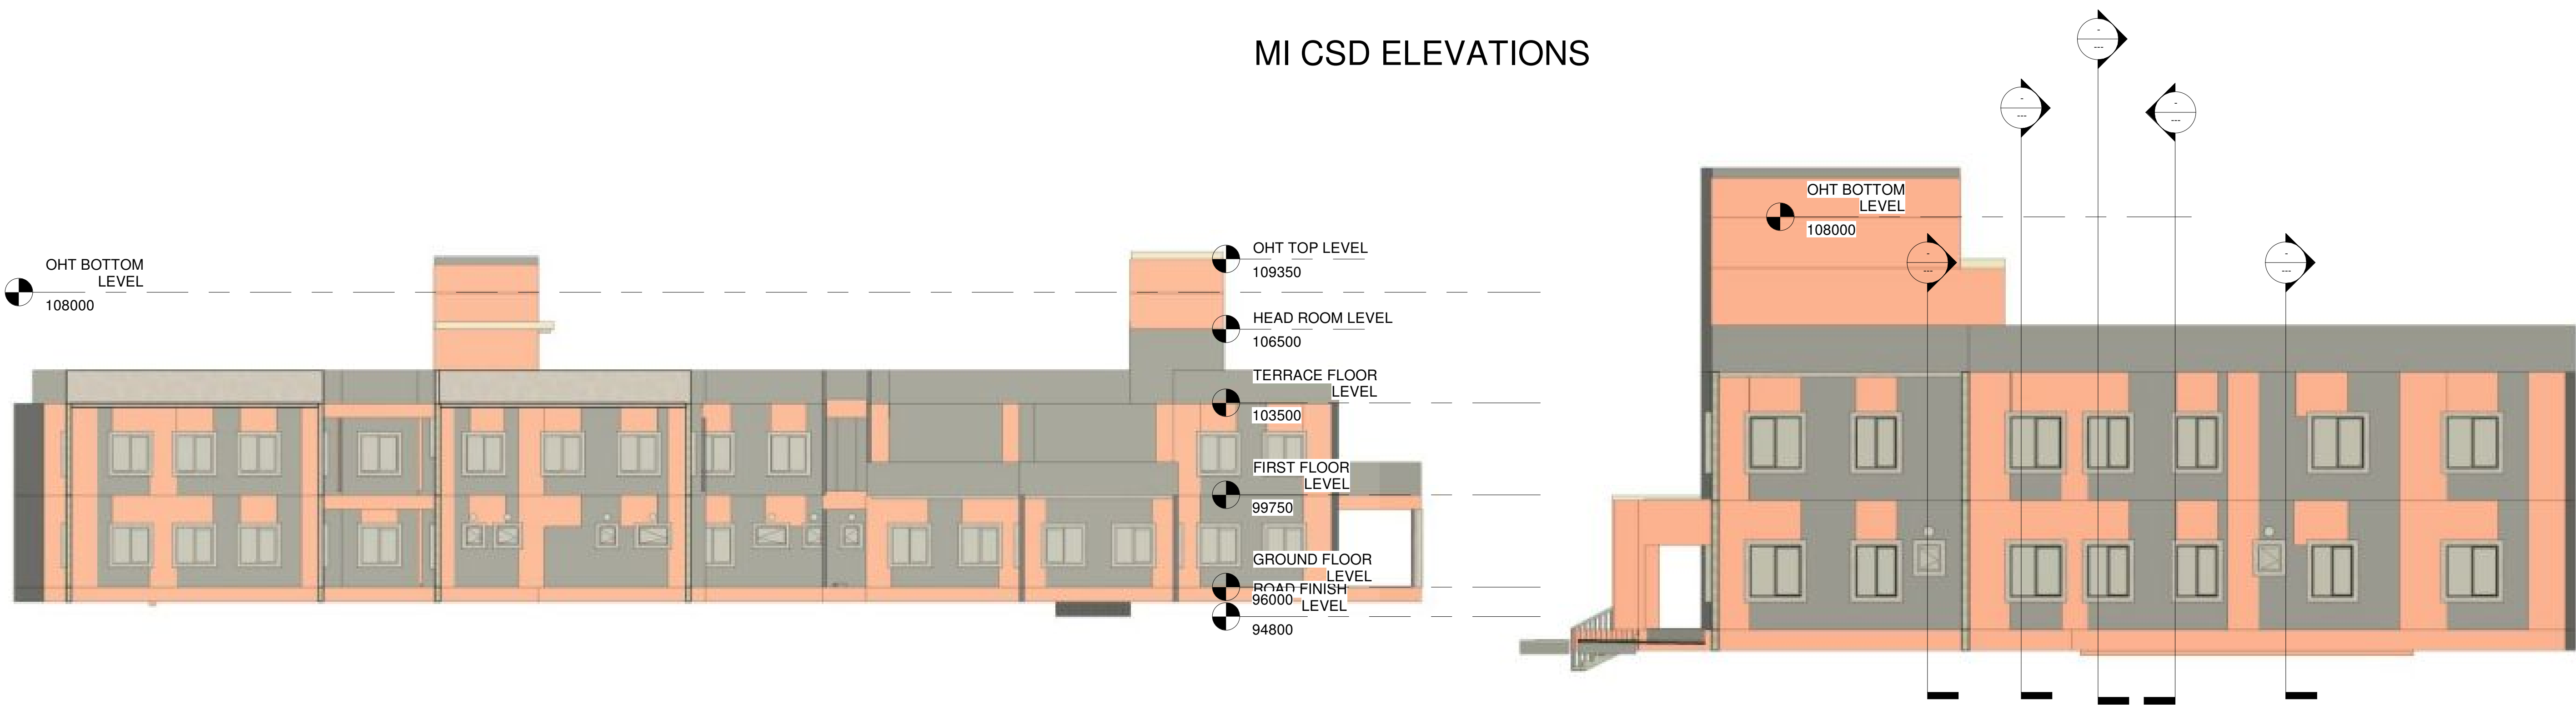

1 North
1 : 140

2 East
1 : 100

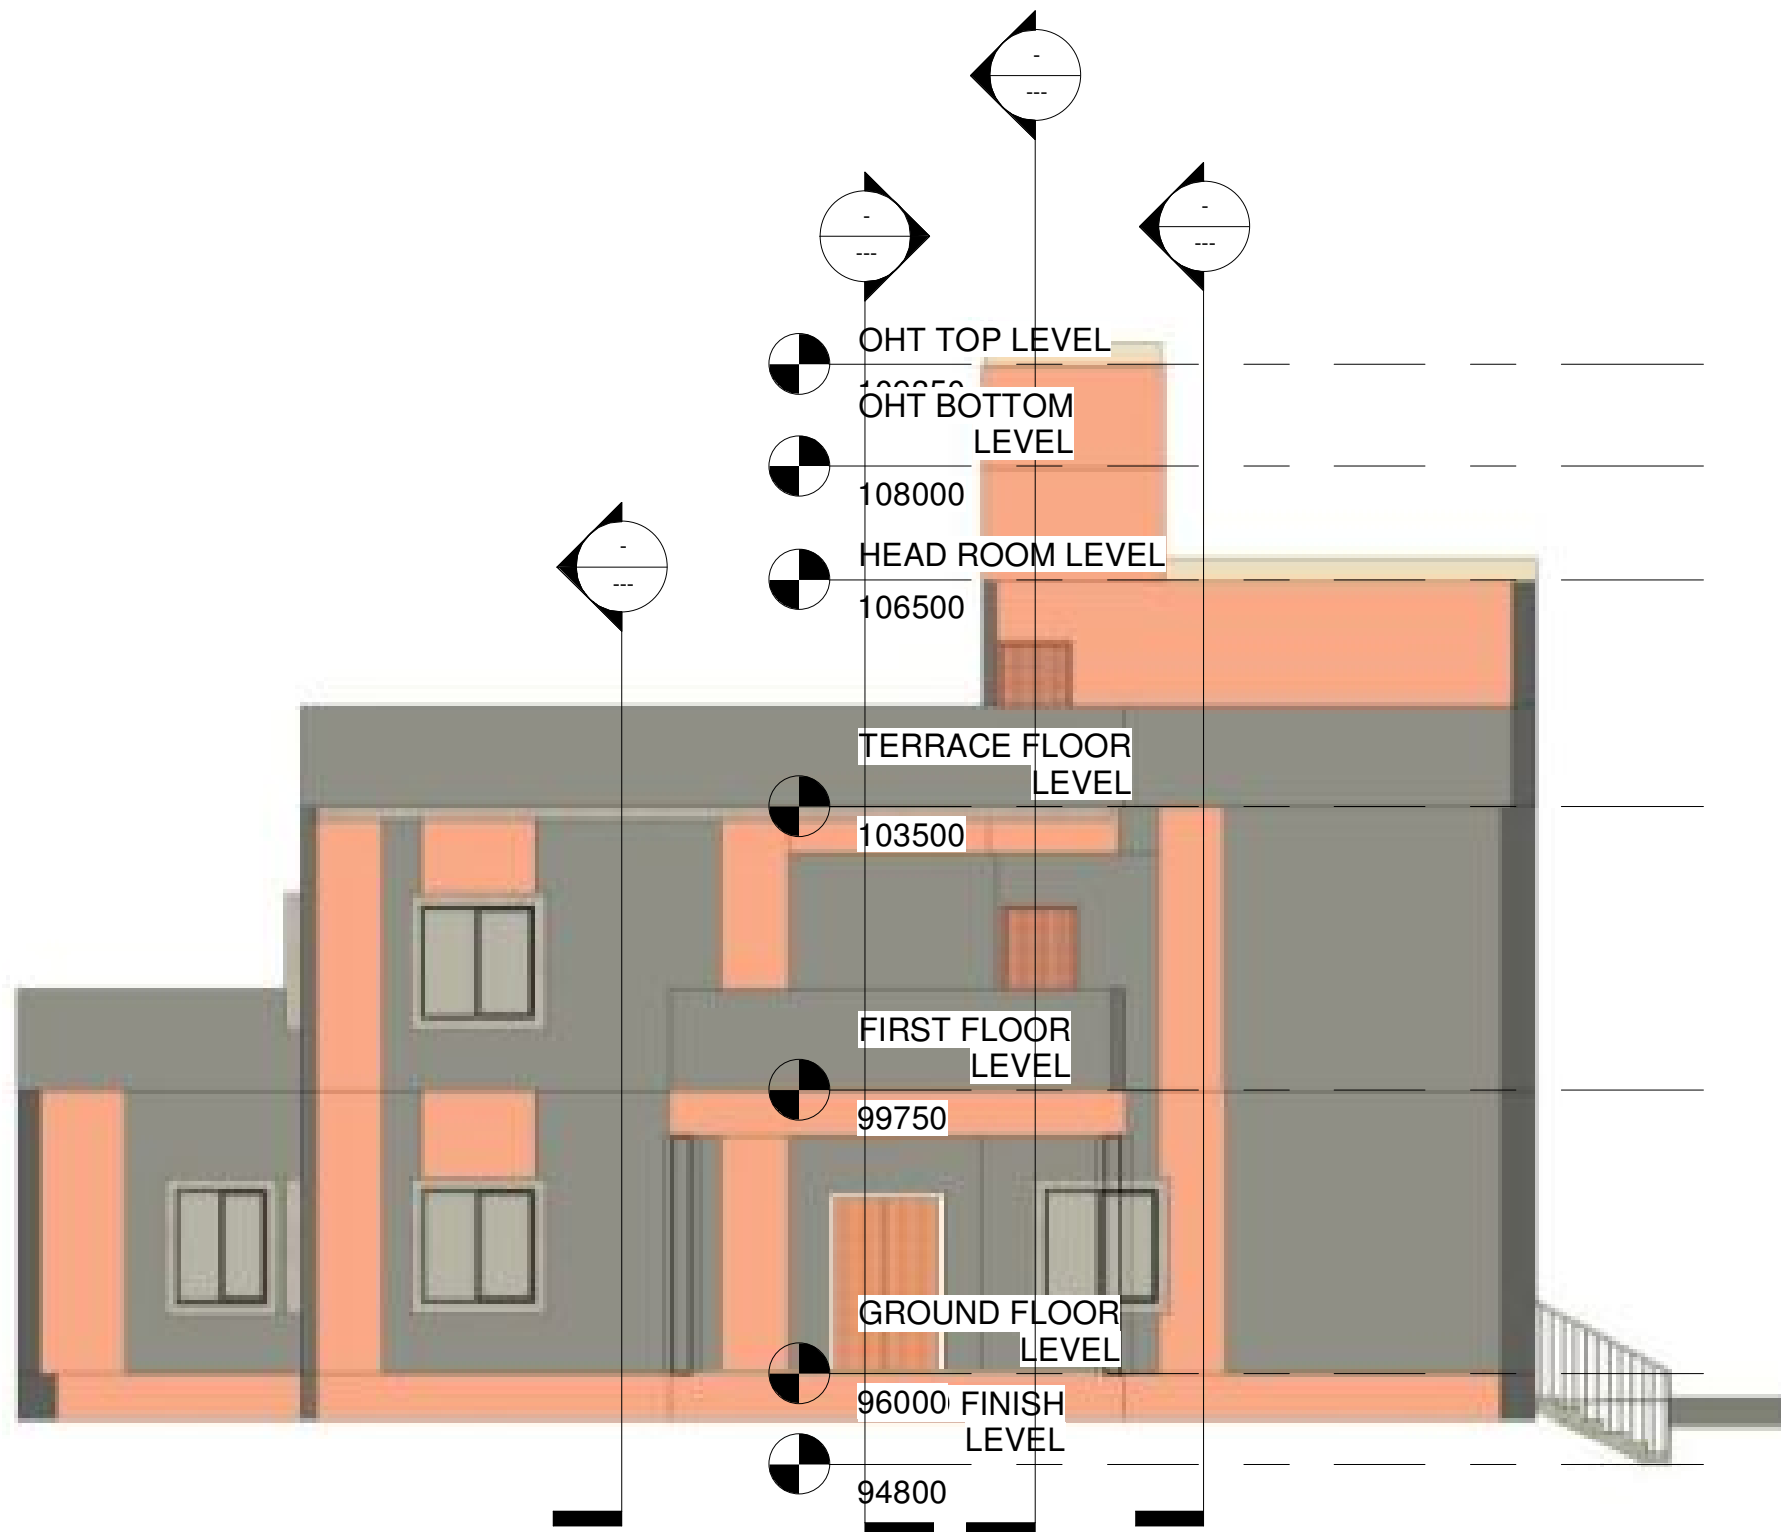

3 West
1 : 100




4 South
1 : 140

PROJECT : NSG CAMPUS

GENERAL NOTES :
1. ALL DIMENSIONS ARE IN MILLIMETER UNLESS STATED OTHERWISE.
2. NO DIMENSION IS TO BE SCALED OFF THE DRAWING.
3. THIS DRAWING TO BE READ IN CONJUNCTION WITH ALL RELEVANT THIS DRAWING TO BE READ IN CONJUNCTION WITH ALL RELEVANT DETAILS.
4. ANY DISCREPANCY IN DRAWING TO BE BROUGHT TO THE NOTICE OF ARCHITECTS BEFORE COMMENCEMENT OF WORK.
5. FOR ALL STAIRS, ELEVATORS, TOILETS - REF SEPARATE DETAILS.
6. FOR ALL SERVICE DRAWINGS - REFER SEPARATE DETAILS.

KEY PLAN:

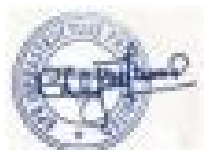

SIGNED/STAMPED BY :
BPR INFRASTRUCTURE PRIVATE LIMITED



SIGNED/STAMPED BY :
B DESIGN STUDIOS

ISSUE/REVISION

IR	DATE	DESCRIPTION

CLIENT

CPWD
CENTRAL PUBLIC WORKS DEPARTMENT

EPC CONTRACTOR

M/S BPR
INFRASTRUCTURE
PRIVATE LIMITED
Plot No. 103 & 104, 1st Floor Capital Park,
Road, Madhapur, Hyderabad, Telangana - 500081.

EPC ARCHITECT

B DESIGN STUDIOS
3rd Floor, ANH Gurni Square Plot No. 328,
100 Feet, Jalandhar, Madhapur,
Hyderabad, Telangana 500081.
Website: www.bdesignstudios.in
Phone: 9440882222

EPC STRUCTURAL & MEP CONSULTANT

SUNV ENGINEERING SERVICES
P/8th & 9th, Madhapur,
Hyderabad,
Telangana 500081
Phone: 92020 8040

PROJECT :

Construction of NSG Regional Hub at Lekhawada,
Gandhinagar, Gujarat.(SH) - Construction of 104
nos
Type-II, 40 nos Type-III, 14 nos Type-IV, 2 nos Type-
V,
1 no. Administrative building cum Lecture hall, 1 no.
Officers mess, 1 no. AC mess, 1 no. 280 men CDO
barrack, 1 no. Quarter Guard, 1 no. MI Room cum
Canteen cum Pre Primary School, 1 no. Electric
substation, 1 no. STP, UG sump and 2 nos. Pump
room
including Internal Water Supply, Sanitary installation
and Electrical work.External Service connection of
Civil
& Electrical, Internal roads, Cement Concrete
pavement, Foot path, Storm water drains, Culverts,
Retaining wall, etc. and all civil services and E & M
services in Engineering, Procurement and
Construction
mode-I, Package-II)
Agreement No: 01/CE/EE/(O)GNR-II/2025-26

BLOCK : MI CSD

DRAWING TITLE : MI CSD ELEVATION

DESIGN : SATHYA APPROVED : RAJESH

SCALE : 1:75 DRAWN : B.MEGHANA

DATE : 16-04-2026 CHECKED : SATHYA

DRAWING NO : A102

PROJECT NO.	SHEET SIZE	CONSTRUCTION	REVISION
006	A1	C	R0

